



U.E.D. 30 USUARIOS Y U.E.N. 9 USUARIOS. MONTEJICAR

PLANTA SEMISÓTANO

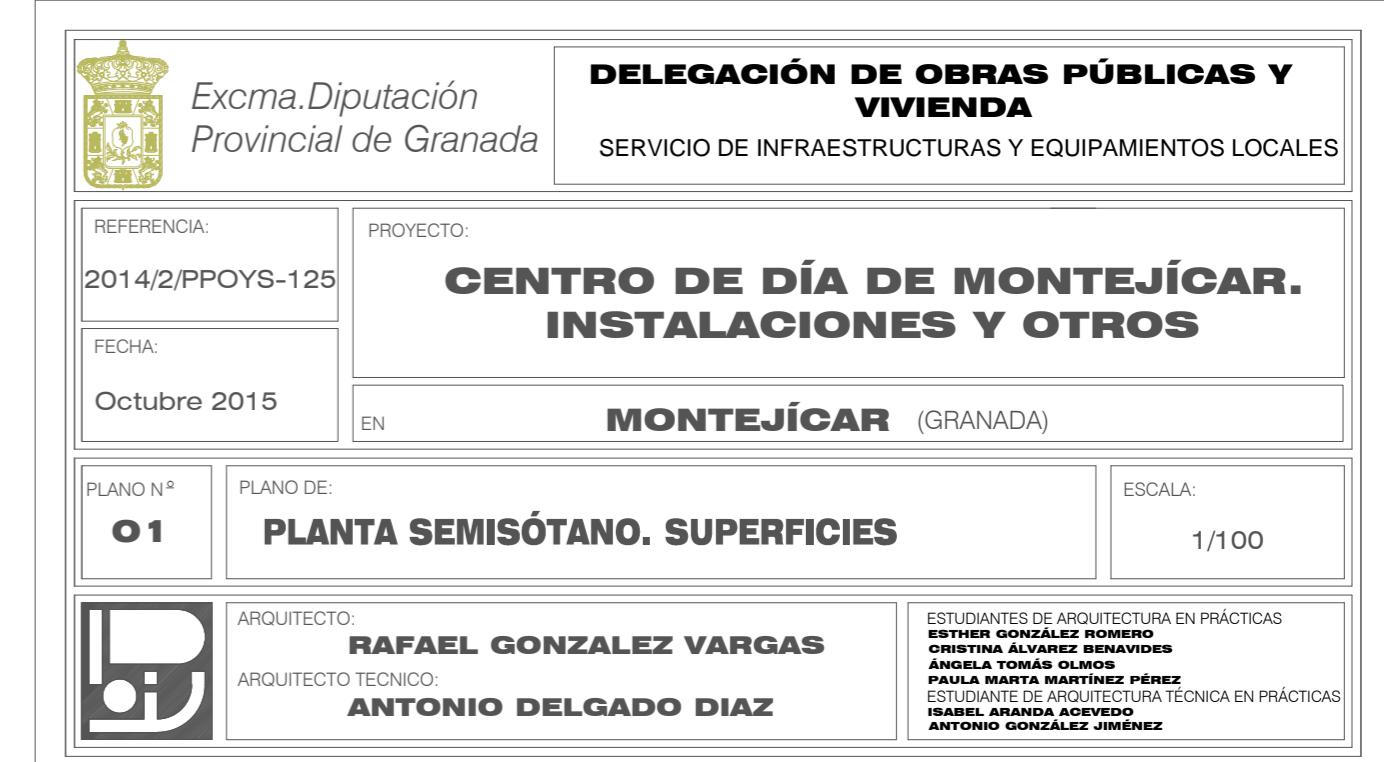

U.E.D. 30 USUARIOS Y U.E.N. 9 USUARIOS. MONTEJICAR

PLANTA SEMISÓTANO

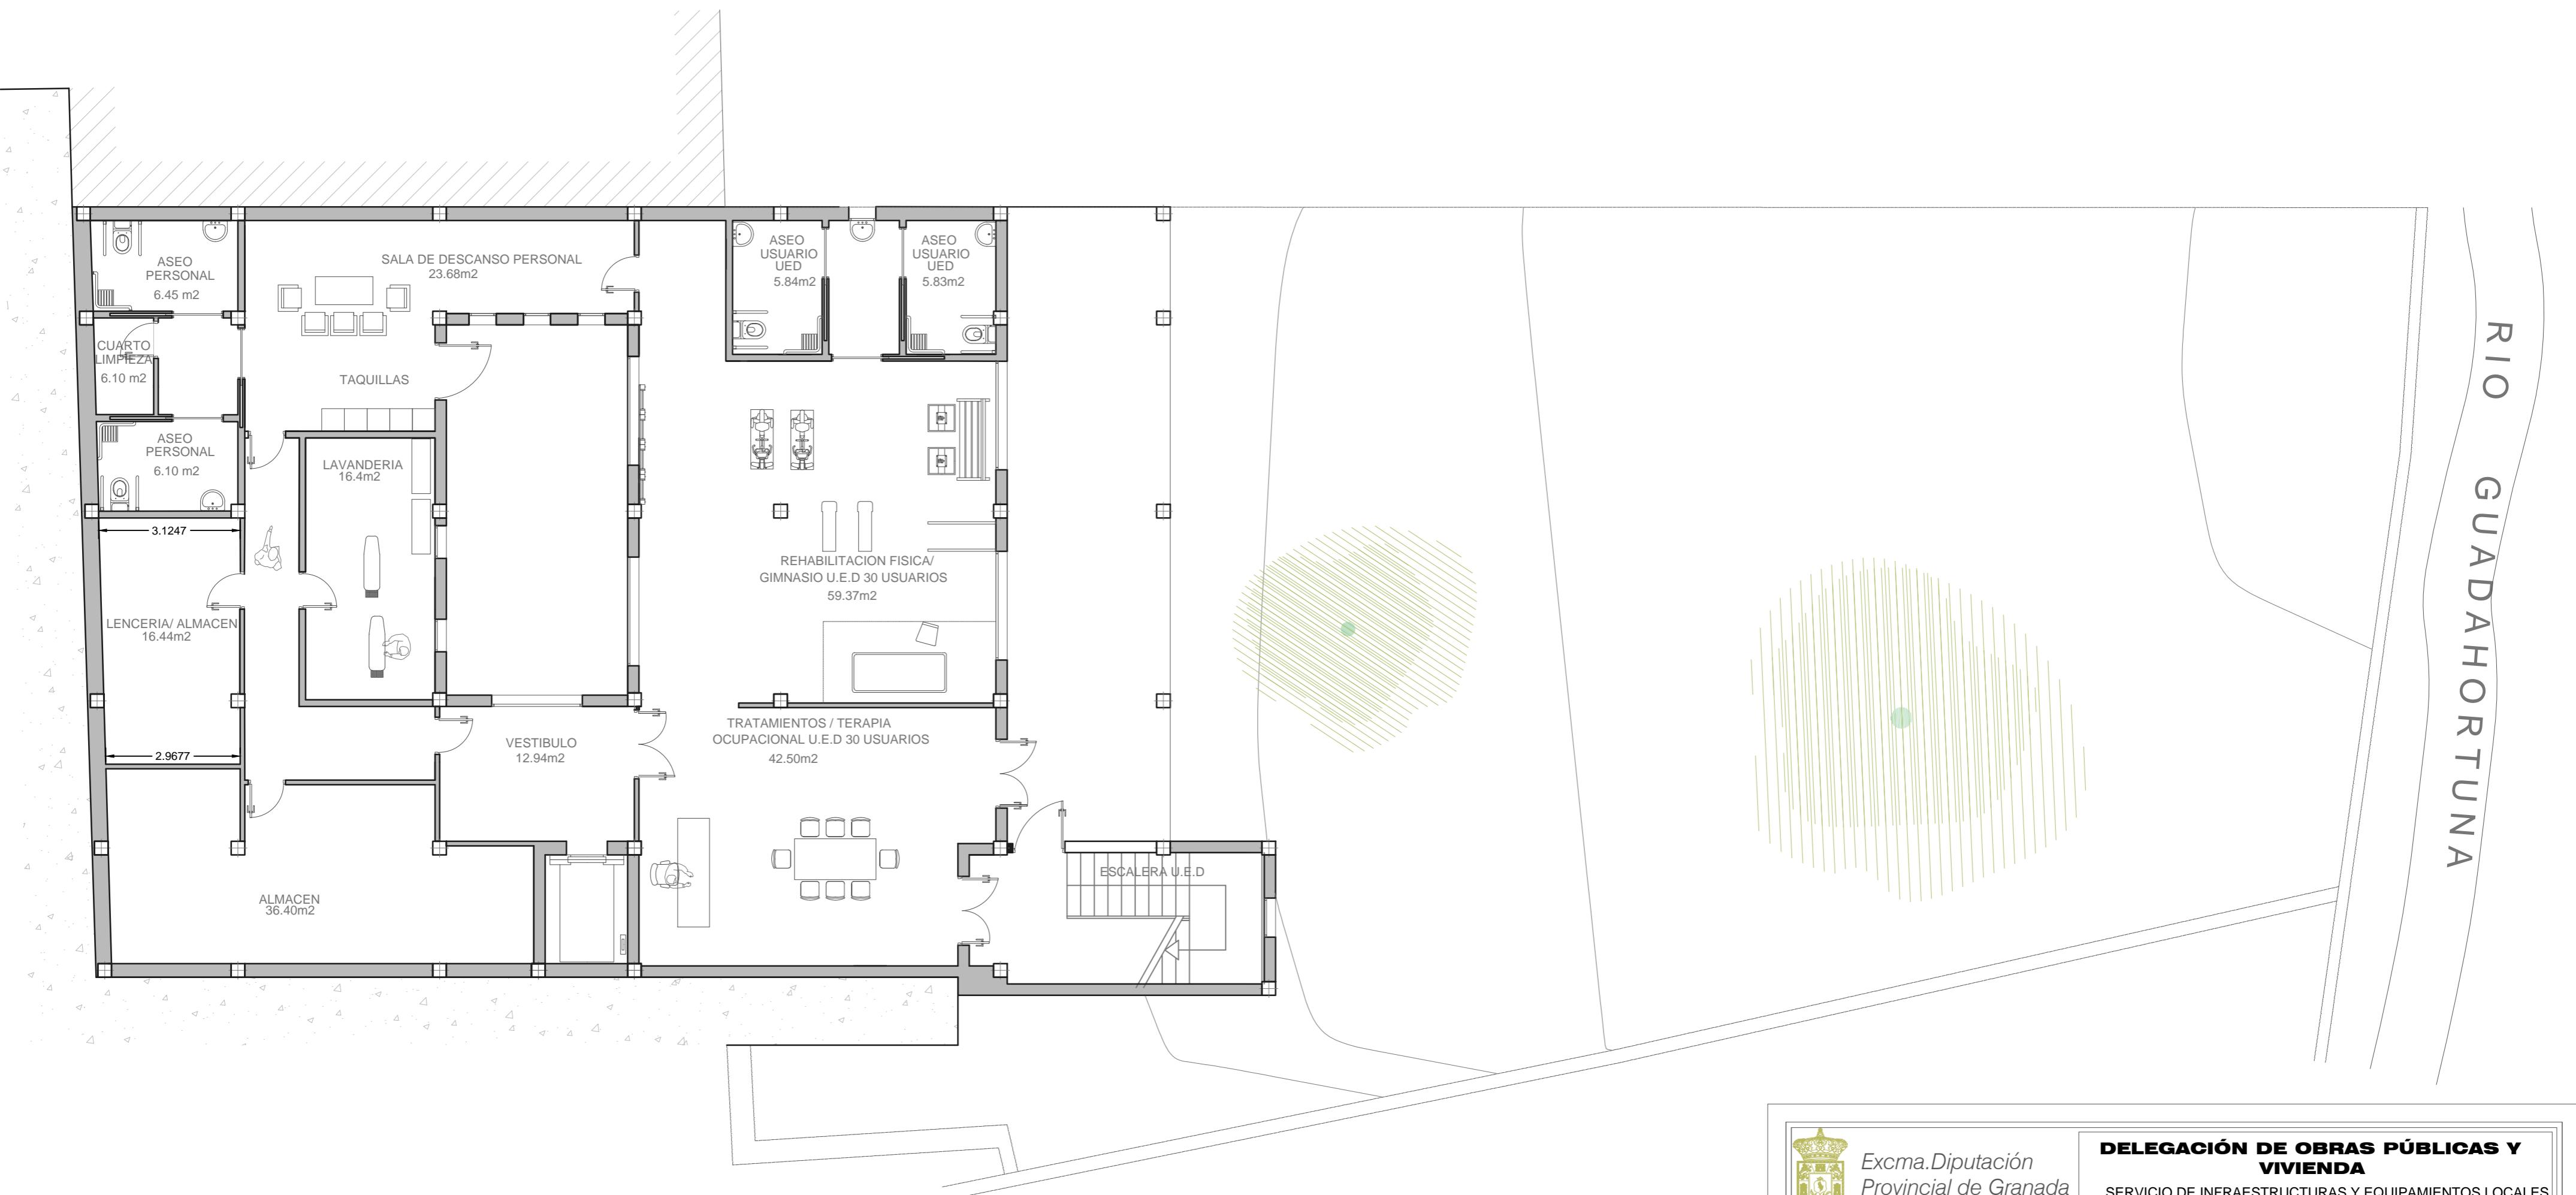


	Excma. Diputación Provincial de Granada	DELEGACIÓN DE OBRAS PÚBLICAS Y VIVIENDA
REFERENCIA: 2014/2/PPOYS-125	PROYECTO: CENTRO DE DÍA DE MONTEJÍCAR. INSTALACIONES Y OTROS	SERVICIO DE INFRAESTRUCTURAS Y EQUIPAMIENTOS LOCALES
FECHA: Octubre 2015	EN	MONTEJÍCAR (GRANADA)
PLANO N° O1	PLANO DE: PLANTA SEMISÓTANO. SUPERFICIES	ESCALA: 1/100
ARQUITECTO: RAFAEL GONZALEZ VARGAS		ESTUDIANTES DE ARQUITECTURA EN PRÁCTICAS ESTHER M. EZ ROMERO CARMONA ALVAREZ SAAVEDRES ANGELA TOMAS OLMO
ARQUITECTO TÉCNICO: ANTONIO DELGADO DIAZ		PAULA MARTA MARTÍNEZ PÉREZ ESTUDIANTE DE ARQUITECTURA TÉCNICA EN PRÁCTICAS ISABEL AGUILAR REVERÓN ANTONIO GONZALEZ JIMÉNEZ

U.E.D. 30 USUARIOS Y U.E.N. 9 USUARIOS. MONTEJICAR


PLANTA BAJA

PILAREJO
CALLE

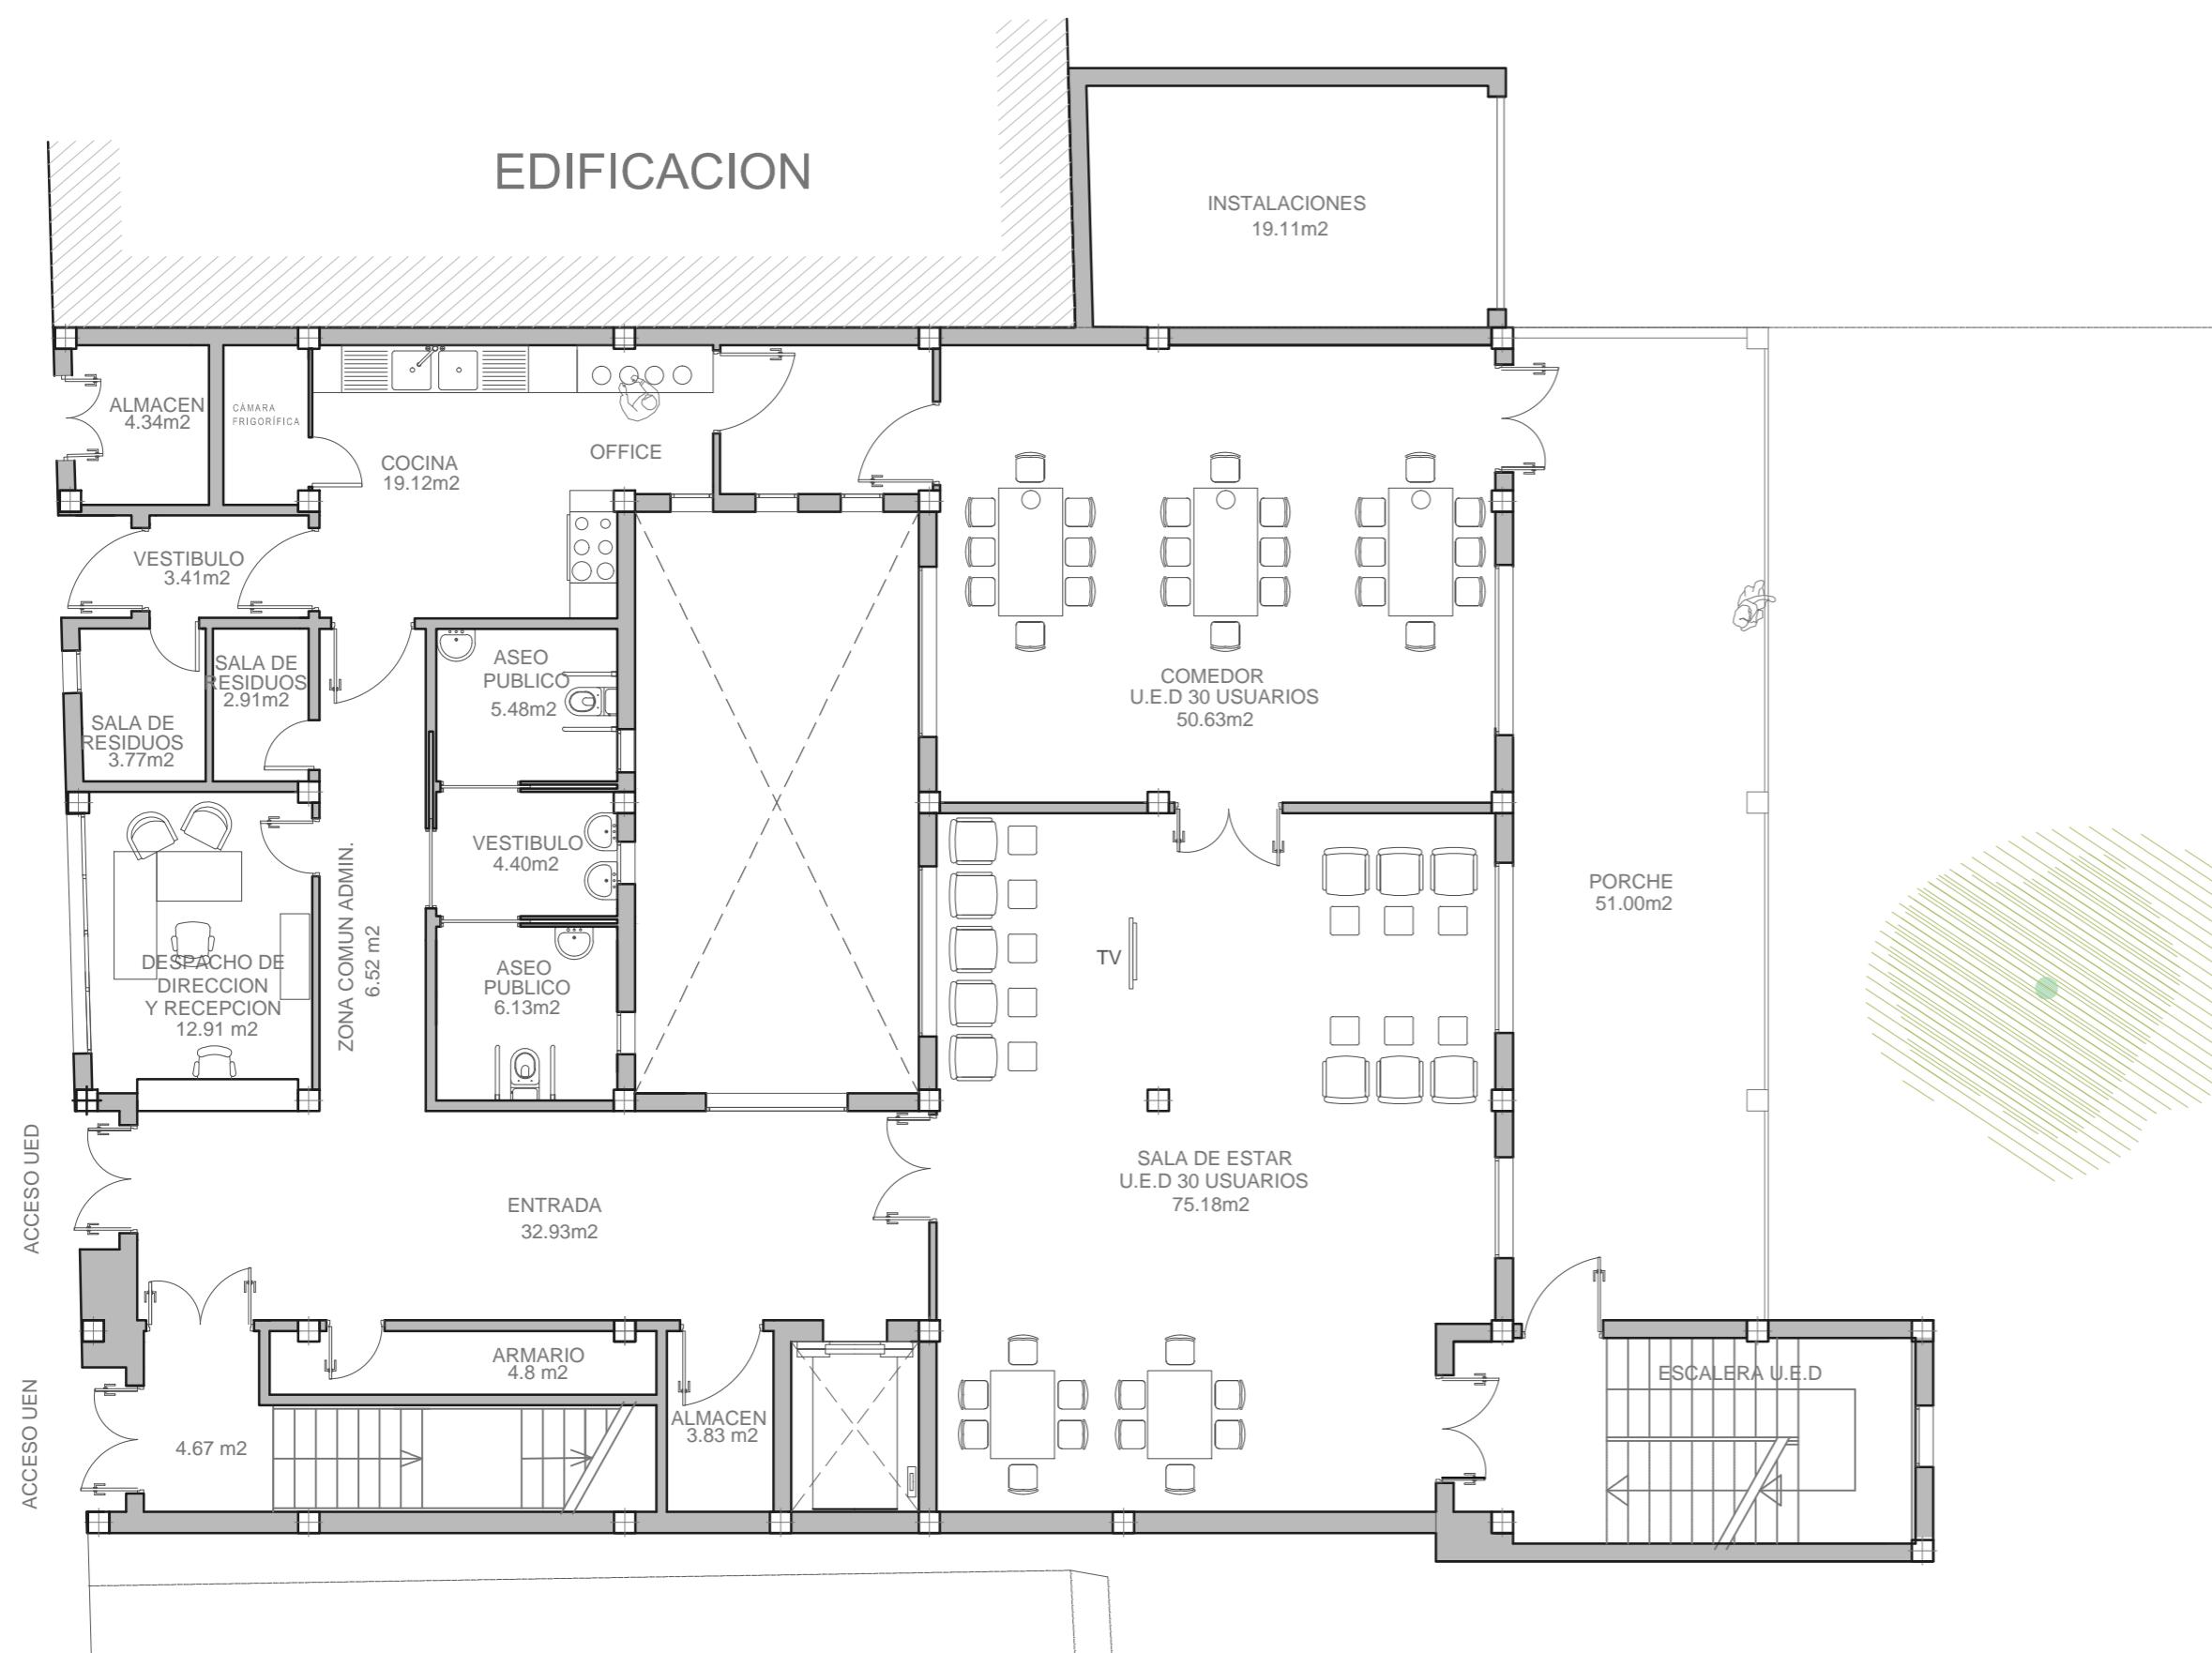

RIO GUADAHORTUNA

	Excma. Diputación Provincial de Granada	DELEGACIÓN DE OBRAS PÚBLICAS Y VIVIENDA
		SERVICIO DE INFRAESTRUCTURAS Y EQUIPAMIENTOS LOCALES
REFERENCIA: 2014/2/PPOYS-125	PROYECTO: CENTRO DE DÍA DE MONTEJÍCAR. INSTALACIONES Y OTROS	
FECHA: Octubre 2015	EN	MONTEJÍCAR (GRANADA)
PLANO N° 02	PLANO DE: PLANTA BAJA. SUPERFICIES	ESCALA: 1/100
		ESTUDIANTES DE ARQUITECTURA EN PRÁCTICAS ESTHER ALVAREZ ROERO CRISTINA ALVAREZ GONZALEZ ANGELA TOMAS OLMO PAULA MARTA MARTINEZ PEREZ ESTUDIANTE DE ARQUITECTURA TÉCNICA EN PRÁCTICAS ISABEL AGUILAR REVERÓN ANTONIO GONZALEZ JIMÉNEZ

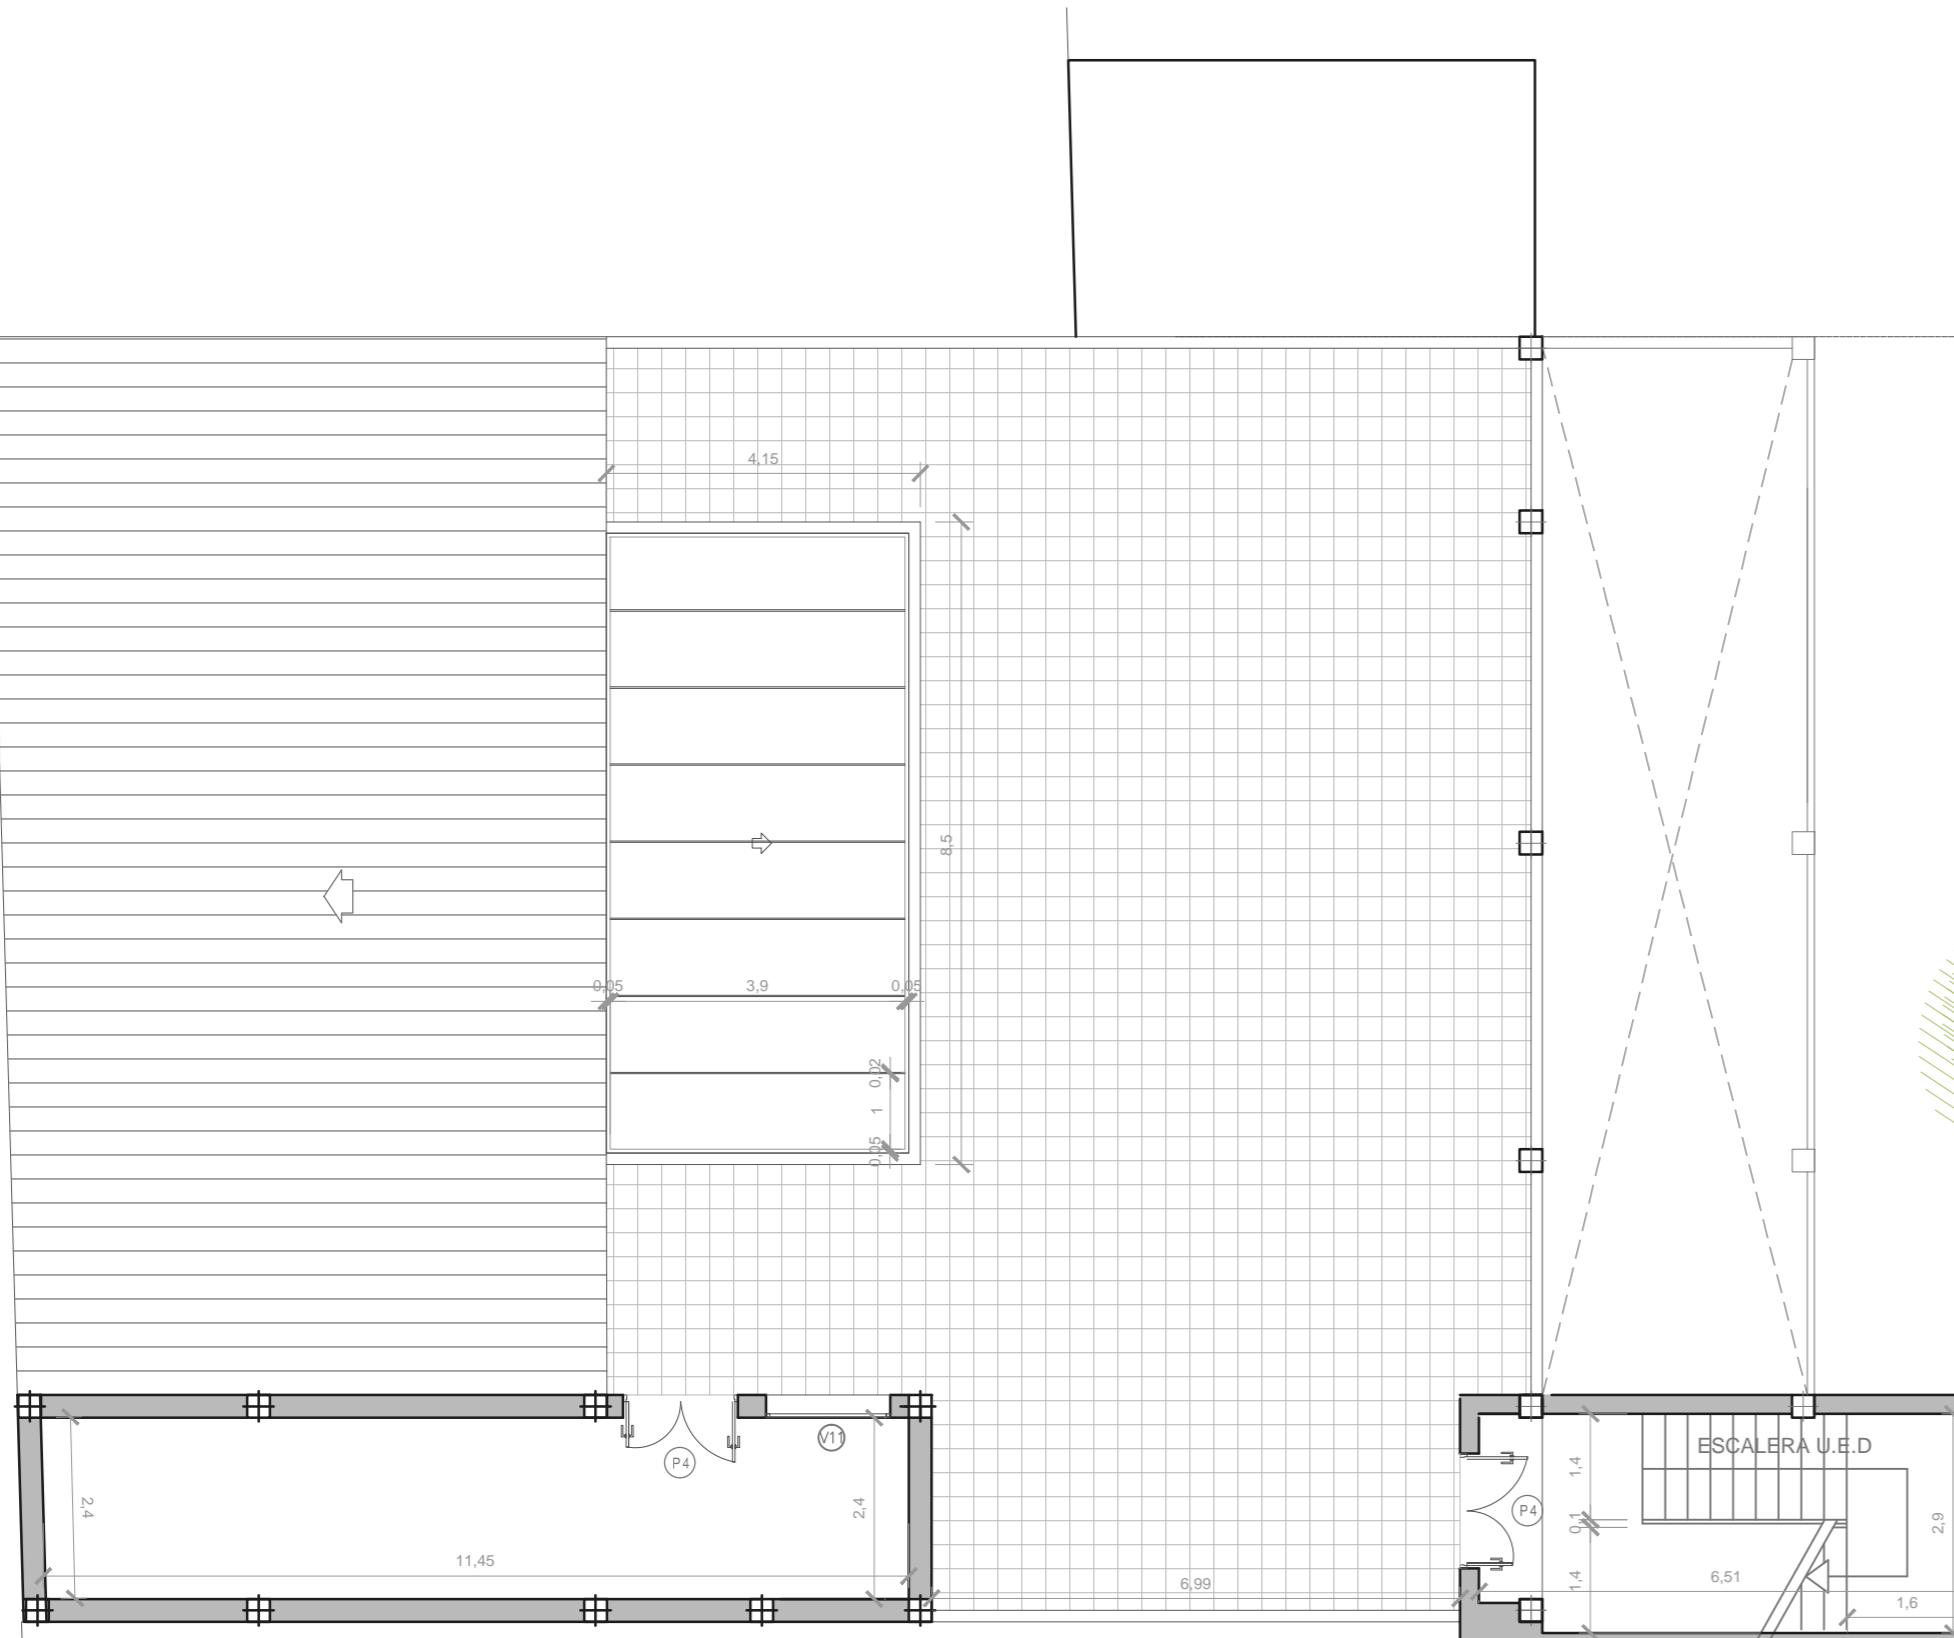

*Excma. Diputación
Provincial de Granada*

DELEGACIÓN DE OBRAS PÚBLICAS Y VIVIENDA

SERVICIO DE INFRAESTRUCTURAS Y EQUIPAMIENTOS LOCALES

REFERENCIA:

2014/2/PPOYS-125

Octubre 2015

'ECTO:

CENTRO DE DÍA DE MONTEJÍCAR. INSTALACIONES Y OTROS

PLANO M

19

PLANO DE:

PLANTA CUBIERTA. ALBAÑILERÍA

ESCALA:

1/100

1


**ARQUITECTO:
RAFAEL GONZALEZ VARGAS**

**ARQUITECTO TECNICO:
ANTONIO DELGADO DIAZ**

ESTUDIANTES DE ARQUITECTURA EN PRÁCTICAS
ESTHER GONZÁLEZ ROMERO
CRISTINA ÁLVAREZ BENAVIDES
ÁNGELA TOMÁS OLMO
PAULA MARTA MARTÍNEZ PÉREZ
ESTUDIANTE DE ARQUITECTURA TÉCNICA EN PRÁCTICAS
ISABEL ARANDA ACEVEDO
ANTONIO GONZÁLEZ JIMÉNEZ

U.E.D. 30 USUARIOS Y U.E.N. 9 USUARIOS. MONTEJICAR


PLANTA PRIMERA

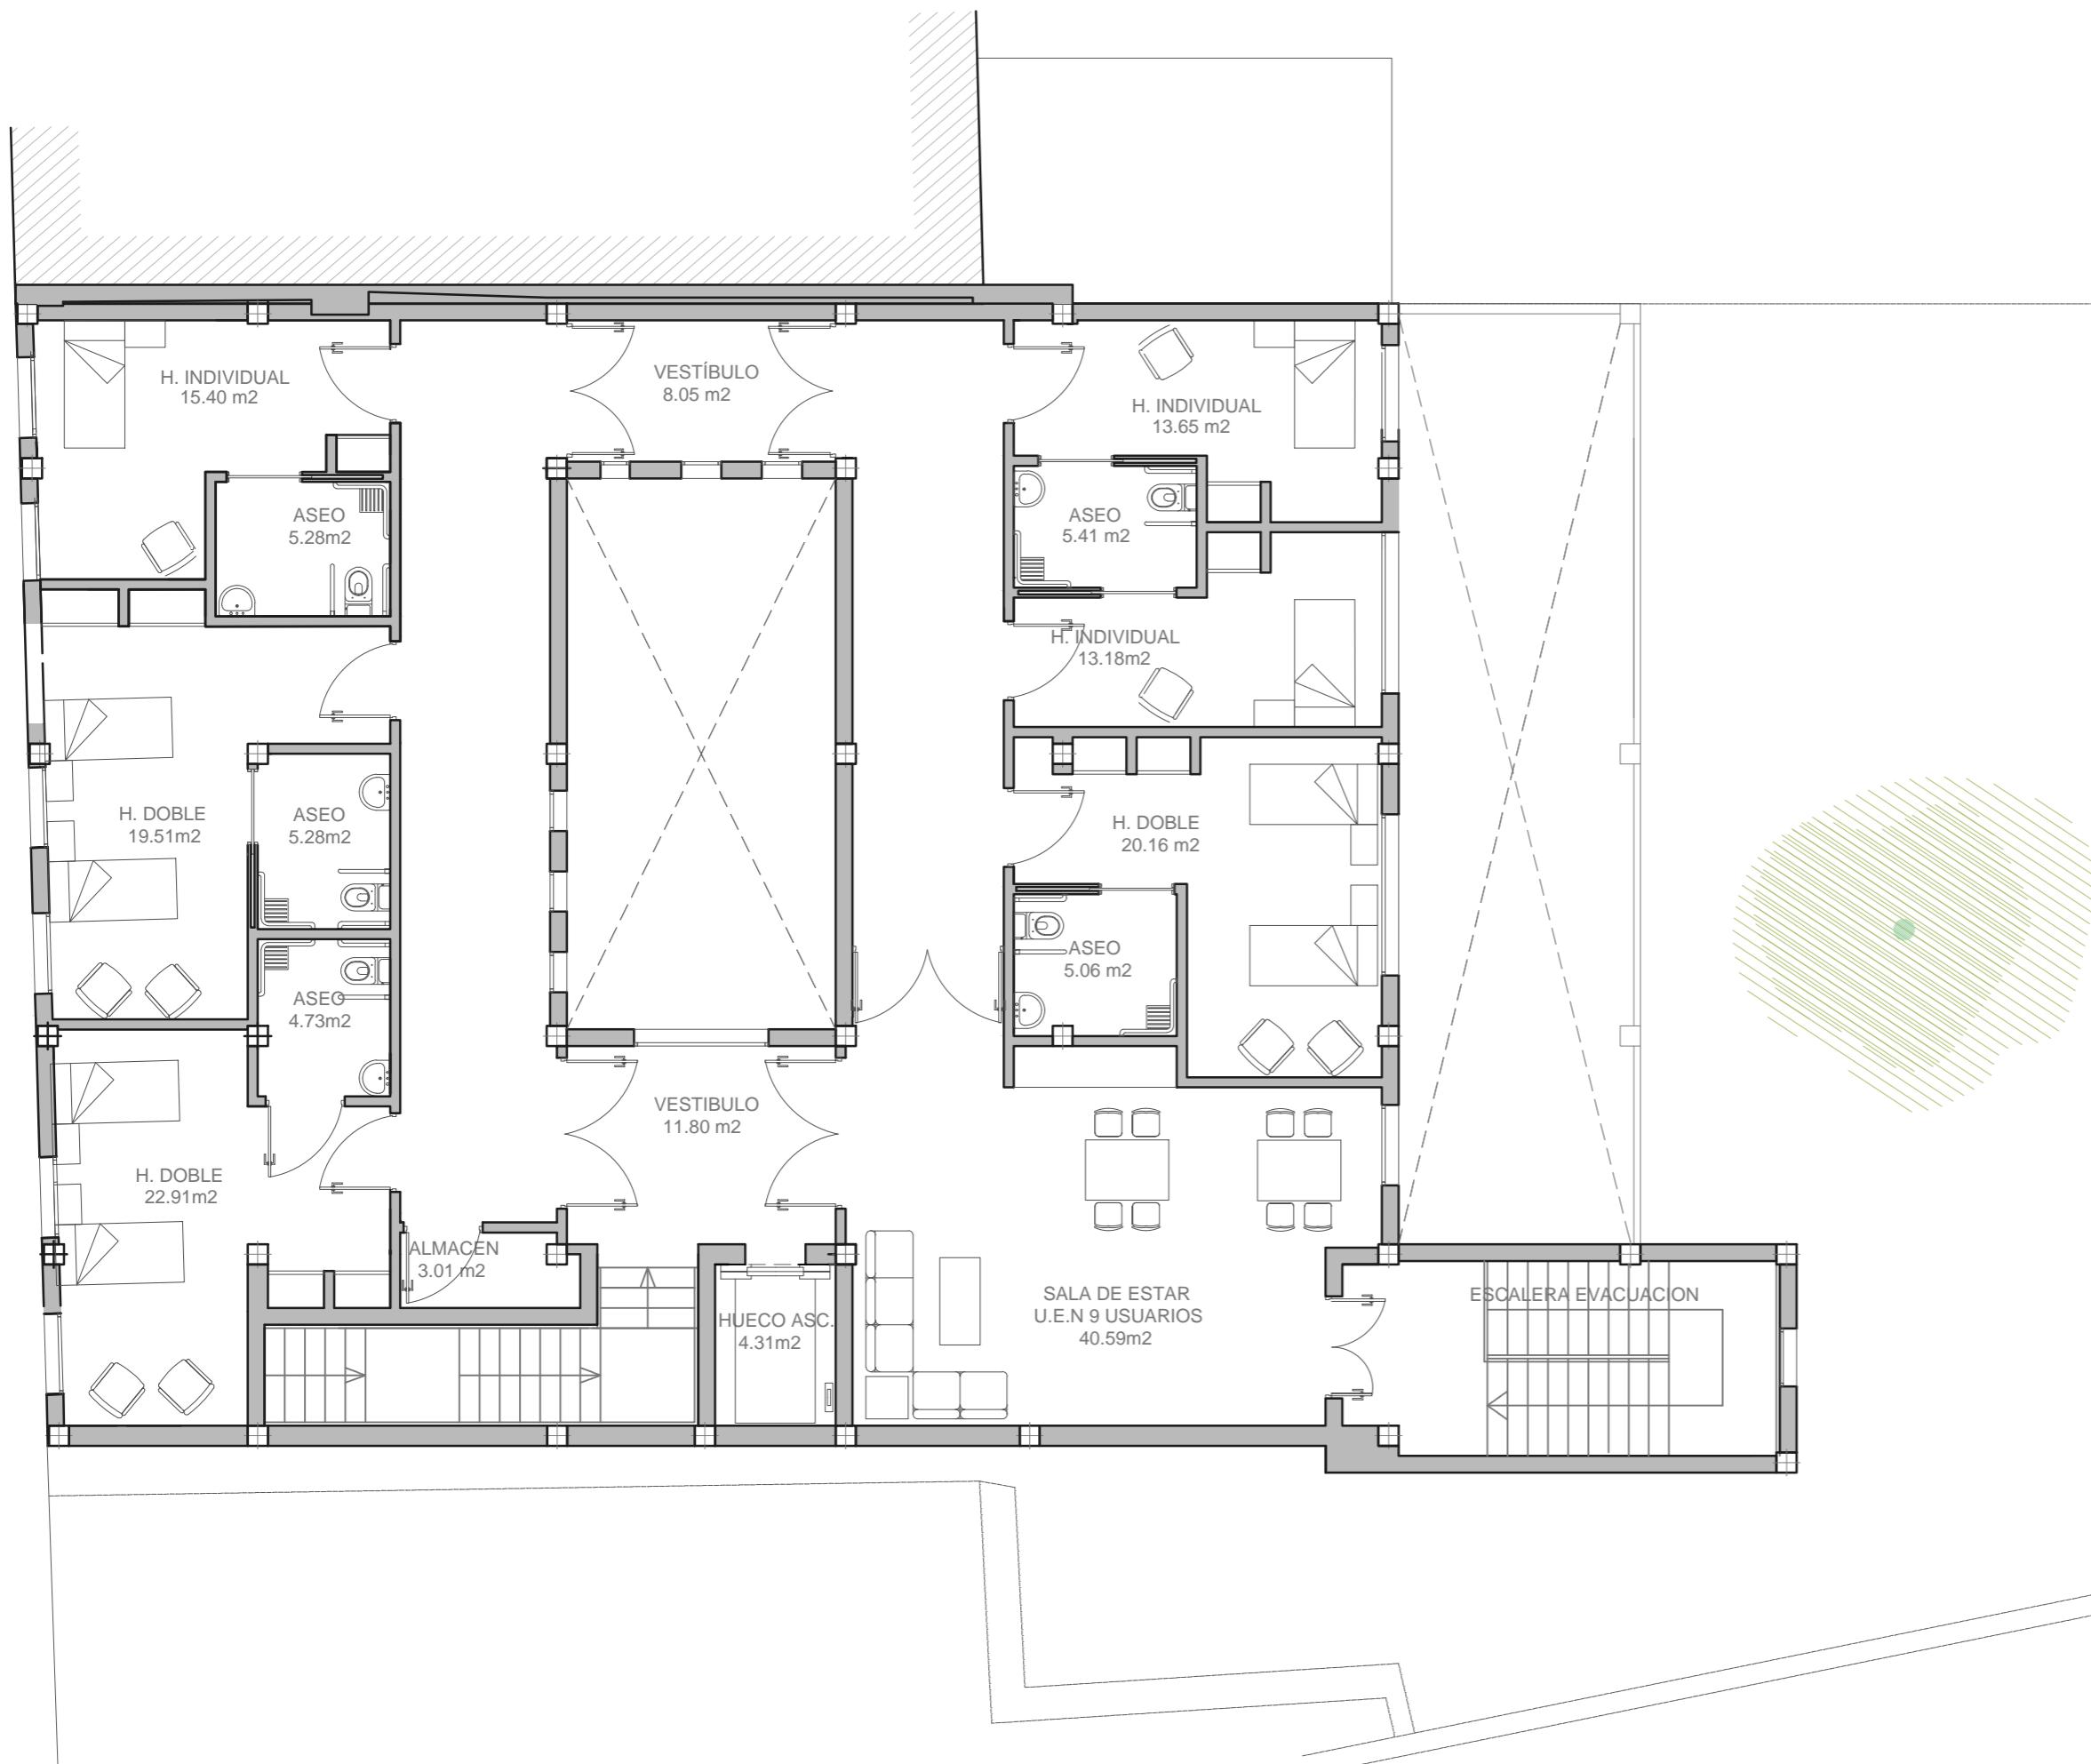


<p>Excma. Diputación Provincial de Granada</p>		DELEGACIÓN DE OBRAS PÚBLICAS Y VIVIENDA SERVICIO DE INFRAESTRUCTURAS Y EQUIPAMIENTOS LOCALES	
REFERENCIA: 2014/2/PPOYS-125	PROYECTO: CENTRO DE DÍA DE MONTEJÍCAR. INSTALACIONES Y OTROS	EN MONTEJÍCAR (GRANADA)	ESCALA: 1/100
PLANO N° 03	PLANO DE: PLANTA PRIMERA. SUPERFICIES		
<p>ARQUITECTO: RAFAEL GONZALEZ VARGAS ARQUITECTO TÉCNICO: ANTONIO DELGADO DIAZ</p>		ESTUDIANTES DE ARQUITECTURA EN PRÁCTICAS ESTER MOLINA ROIGERO CRISTINA ALVAREZ GONZÁLEZ ANGELA TOMAS OLMO PAULA MARTA MARTÍNEZ PÉREZ ESTUDIANTE DE ARQUITECTURA TÉCNICA EN PRÁCTICAS ISABEL ARANDA ACEVEDO ANTONIO GONZALEZ JIMÉNEZ	

U.E.D. 30 USUARIOS Y U.E.N. 9 USUARIOS. MONTEJICAR

PLANTA CUBIERTAS

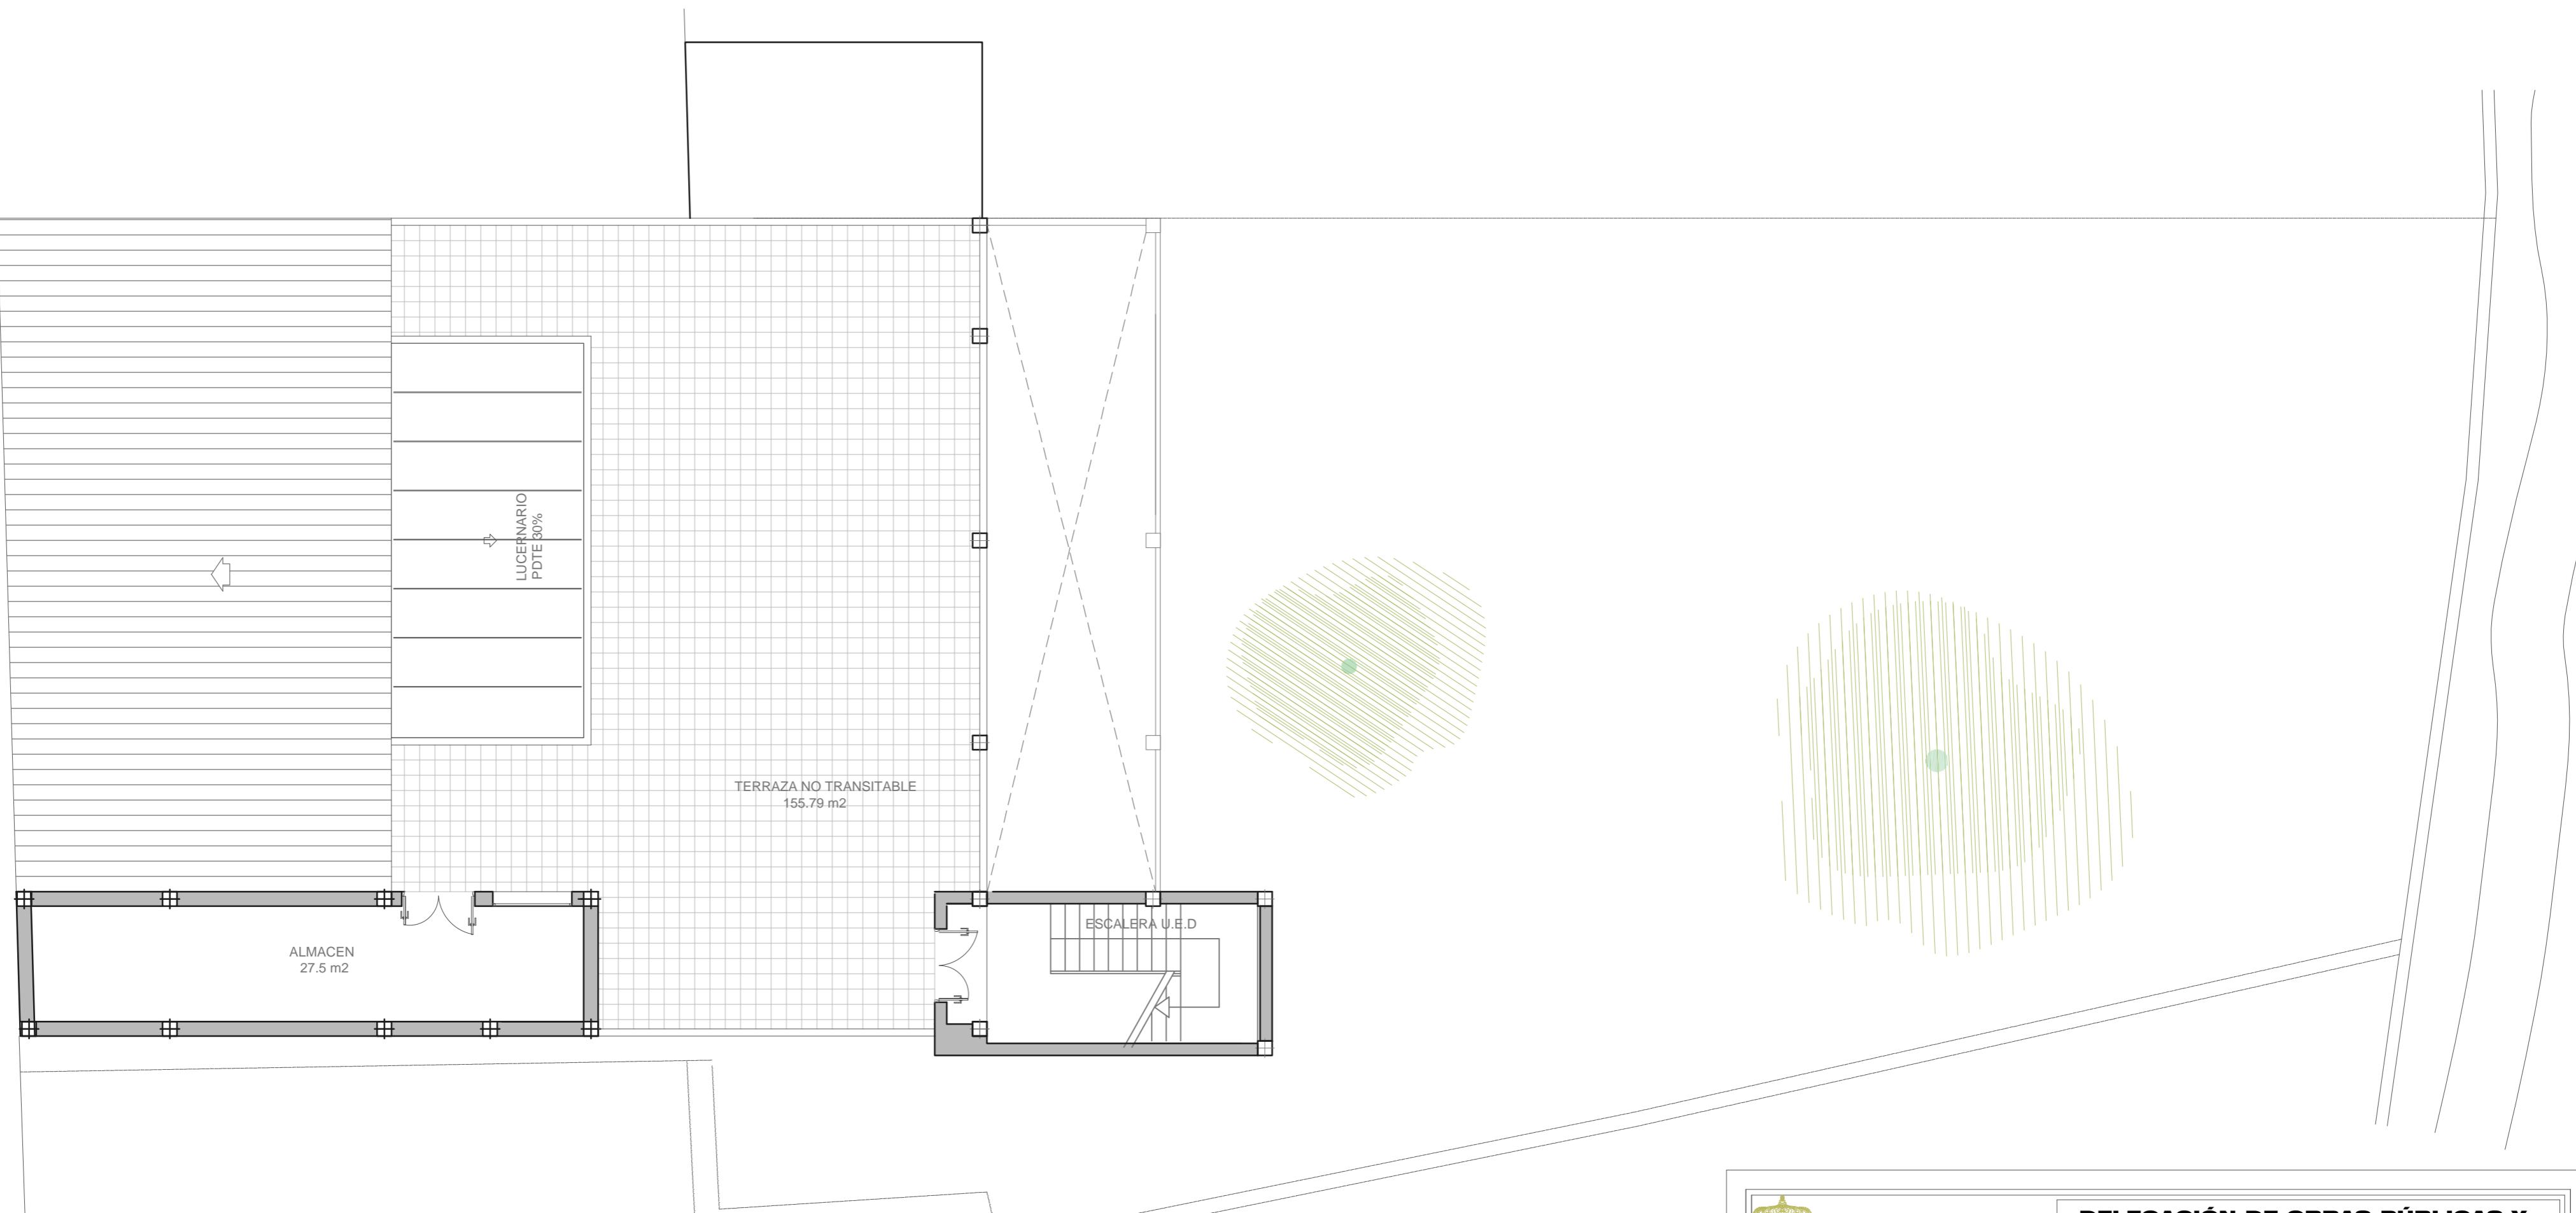


	Excma. Diputación Provincial de Granada		DELEGACIÓN DE OBRAS PÚBLICAS Y VIVIENDA	
REFERENCIA: 2014/2/PPOYS-125		PROYECTO: CENTRO DE DÍA DE MONTEJÍCAR. INSTALACIONES Y OTROS		SERVICIO DE INFRAESTRUCTURAS Y EQUIPAMIENTOS LOCALES
FECHA: Octubre 2015		EN MONTEJÍCAR (GRANADA)		PLANO N° 04
PLANO DE: PLANTA CUBIERTAS. SUPERFICIES		PLANO DE: PLANTA CUBIERTAS. SUPERFICIES		ESCALA: 1/100
		ARQUITECTO: RAFAEL GONZALEZ VARGAS		ESTUDIANTES DE ARQUITECTURA EN PRÁCTICAS ESTER MOLINA RODERO CRISTINA ALVAREZ GONZÁLEZ ANGELA TOMAS OLMO PAULA MARTA MARTÍNEZ PÉREZ ESTER GARCÍA ALVAREZ ISABEL ARANDA ACEVEDO ANTONIO GONZALEZ JIMÉNEZ
		ARQUITECTO TÉCNICO: ANTONIO DELGADO DÍAZ		

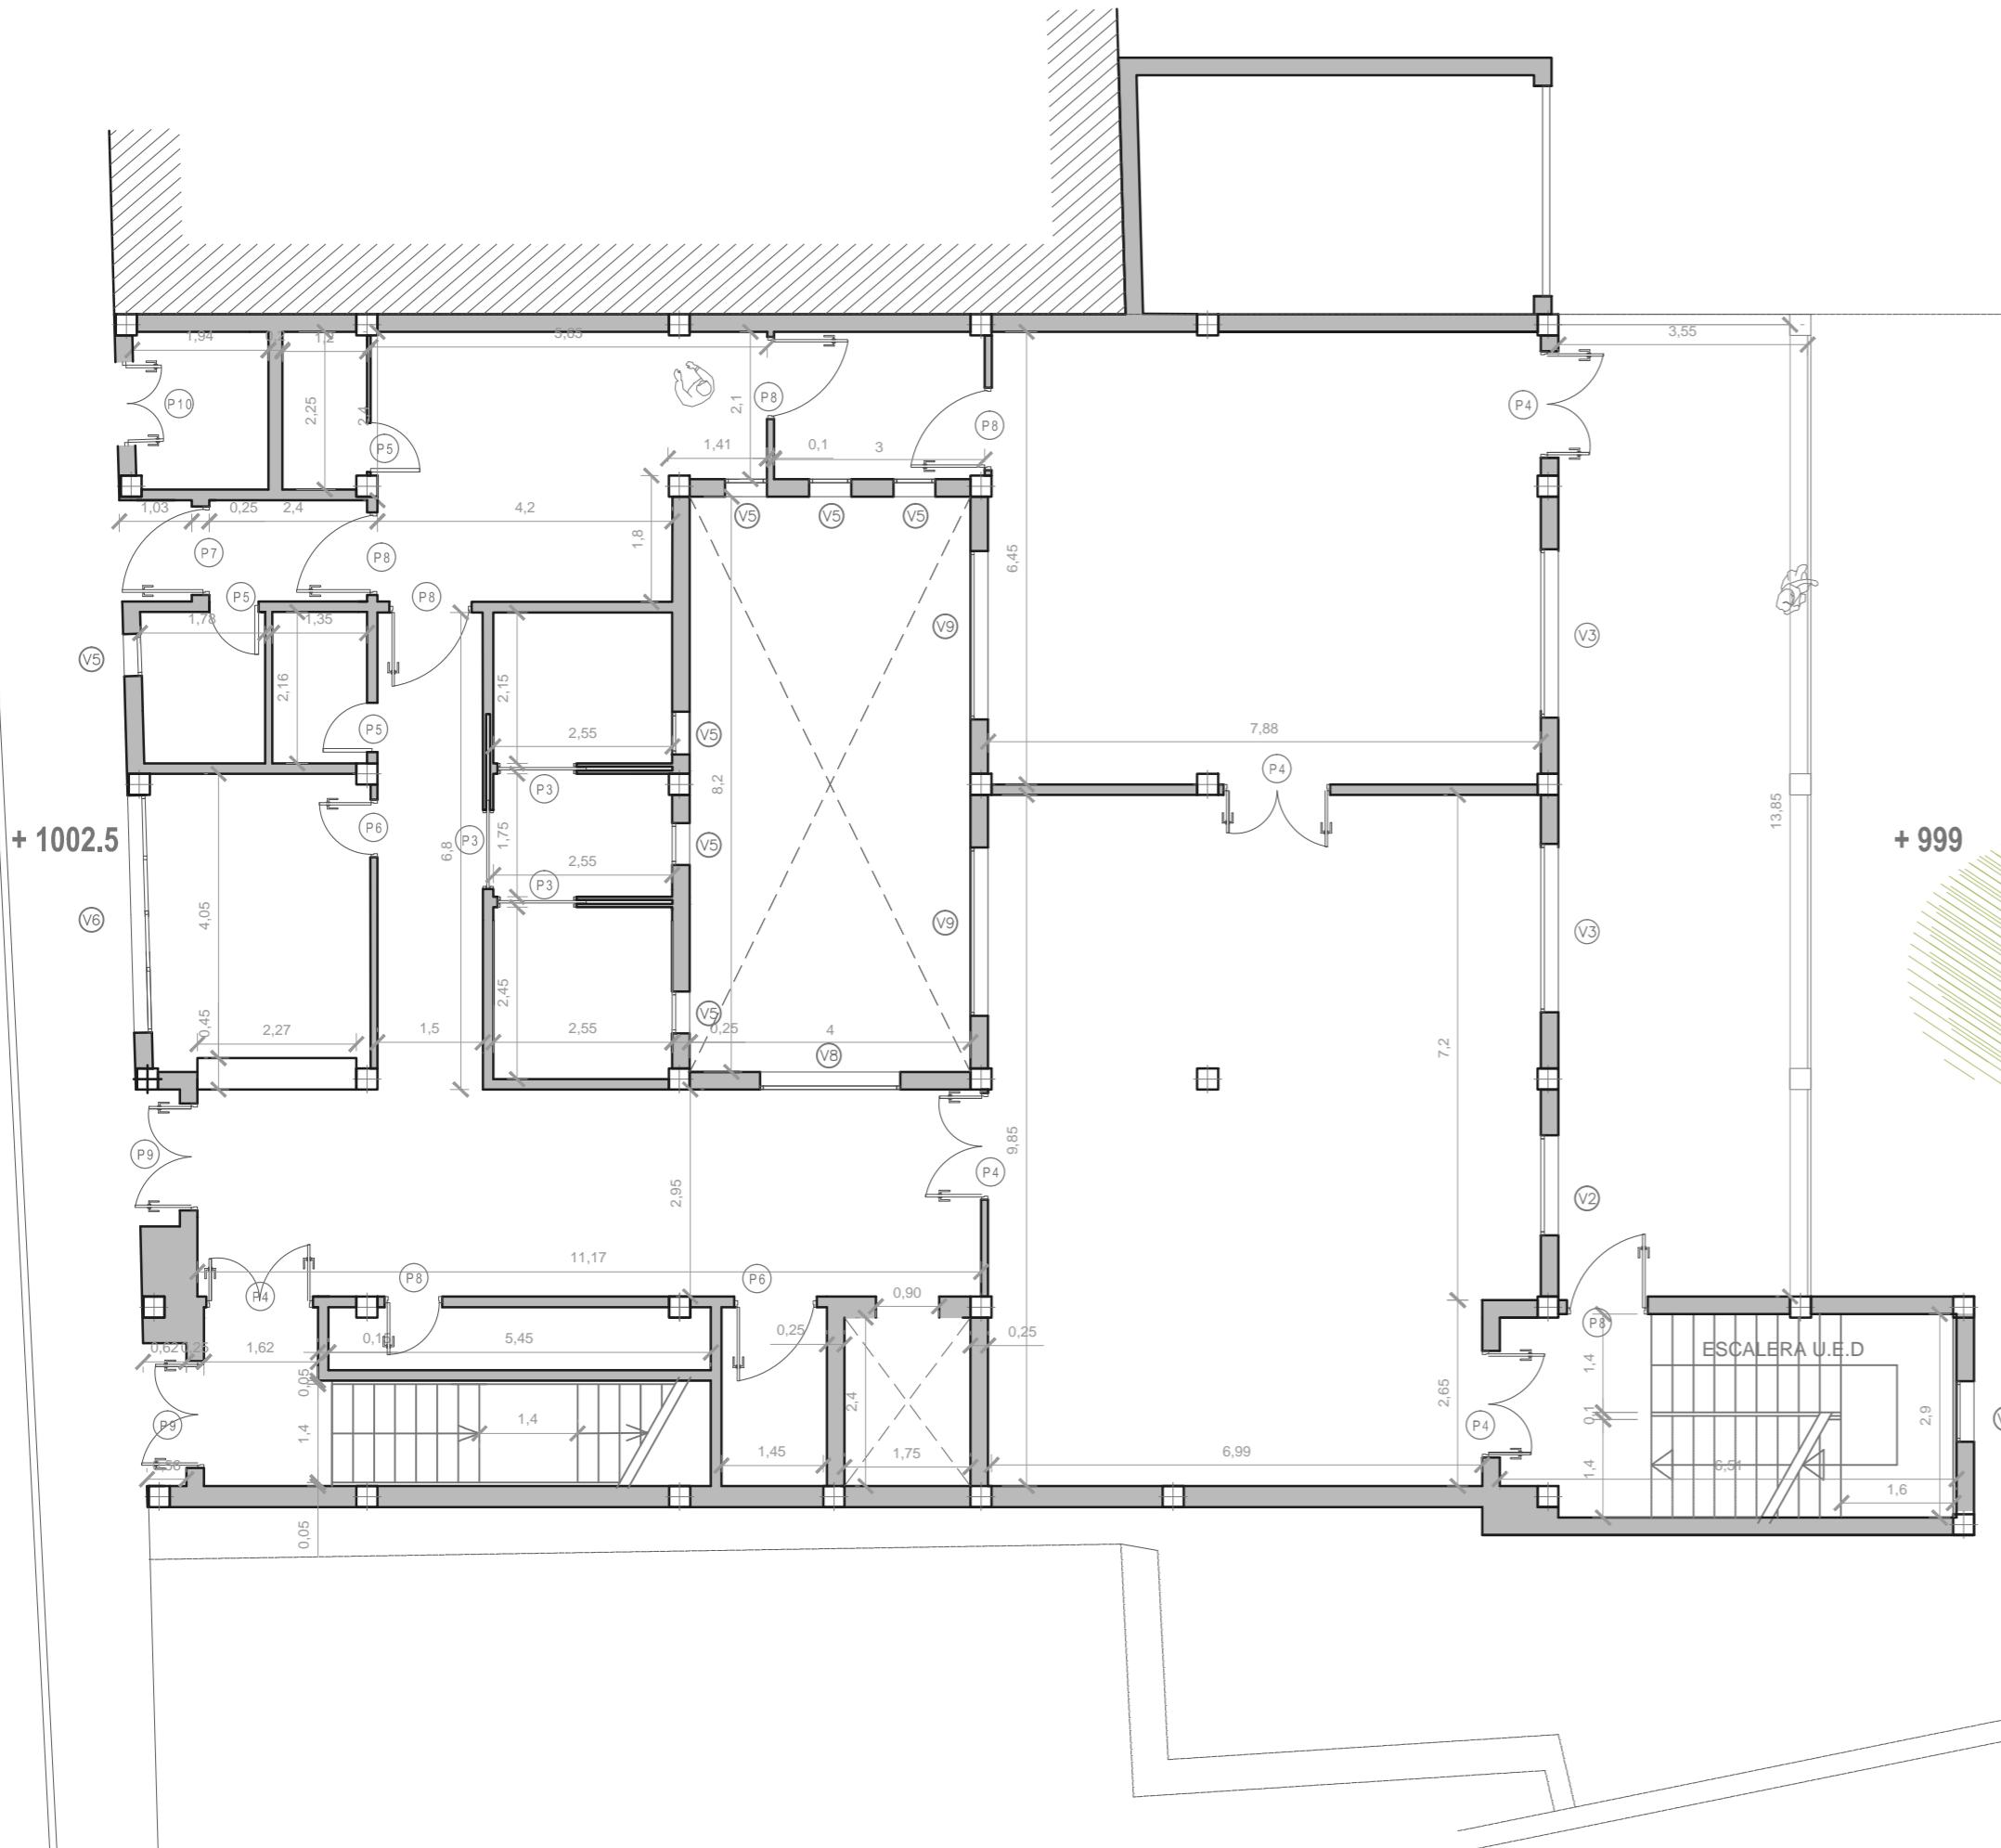

<p>Excma. Diputación Provincial de Granada</p>		DELEGACIÓN DE OBRAS PÚBLICAS Y VIVIENDA SERVICIO DE INFRAESTRUCTURAS Y EQUIPAMIENTOS LOCALES	
REFERENCIA:	PROYECTO:		
2014/2/PPOYS-125	CENTRO DE DÍA DE MONTEJÍCAR. INSTALACIONES Y OTROS		
FECHA:	EN MONTEJÍCAR (GRANADA)		
Octubre 2015	PLANO N°	PLANO DE:	ESCALA:
08	PLANTA BAJA. ALBAÑILERÍA		1/100
		ARQUITECTO: RAFAEL GONZALEZ VARGAS ARQUITECTO TÉCNICO: ANTONIO DELGADO DIAZ	
<small>ESTUDIANTES DE ARQUITECTURA EN PRÁCTICAS ESTEBAN ALVAREZ RODERO CRISTINA ALVAREZ GONZÁLEZ ANGELA TOMAS OLMO PAULA MARTA MARTÍNEZ PÉREZ ESTUDIANTES DE ARQUITECTURA TÉCNICA EN PRÁCTICAS ISABEL ARANDA ACEVEDO ANTONIO GONZALEZ JIMÉNEZ</small>			

U.E.D. 30 USUARIOS Y U.E.N. 9 USUARIOS. MONTEJICAR

PLANTA CUBIERTAS

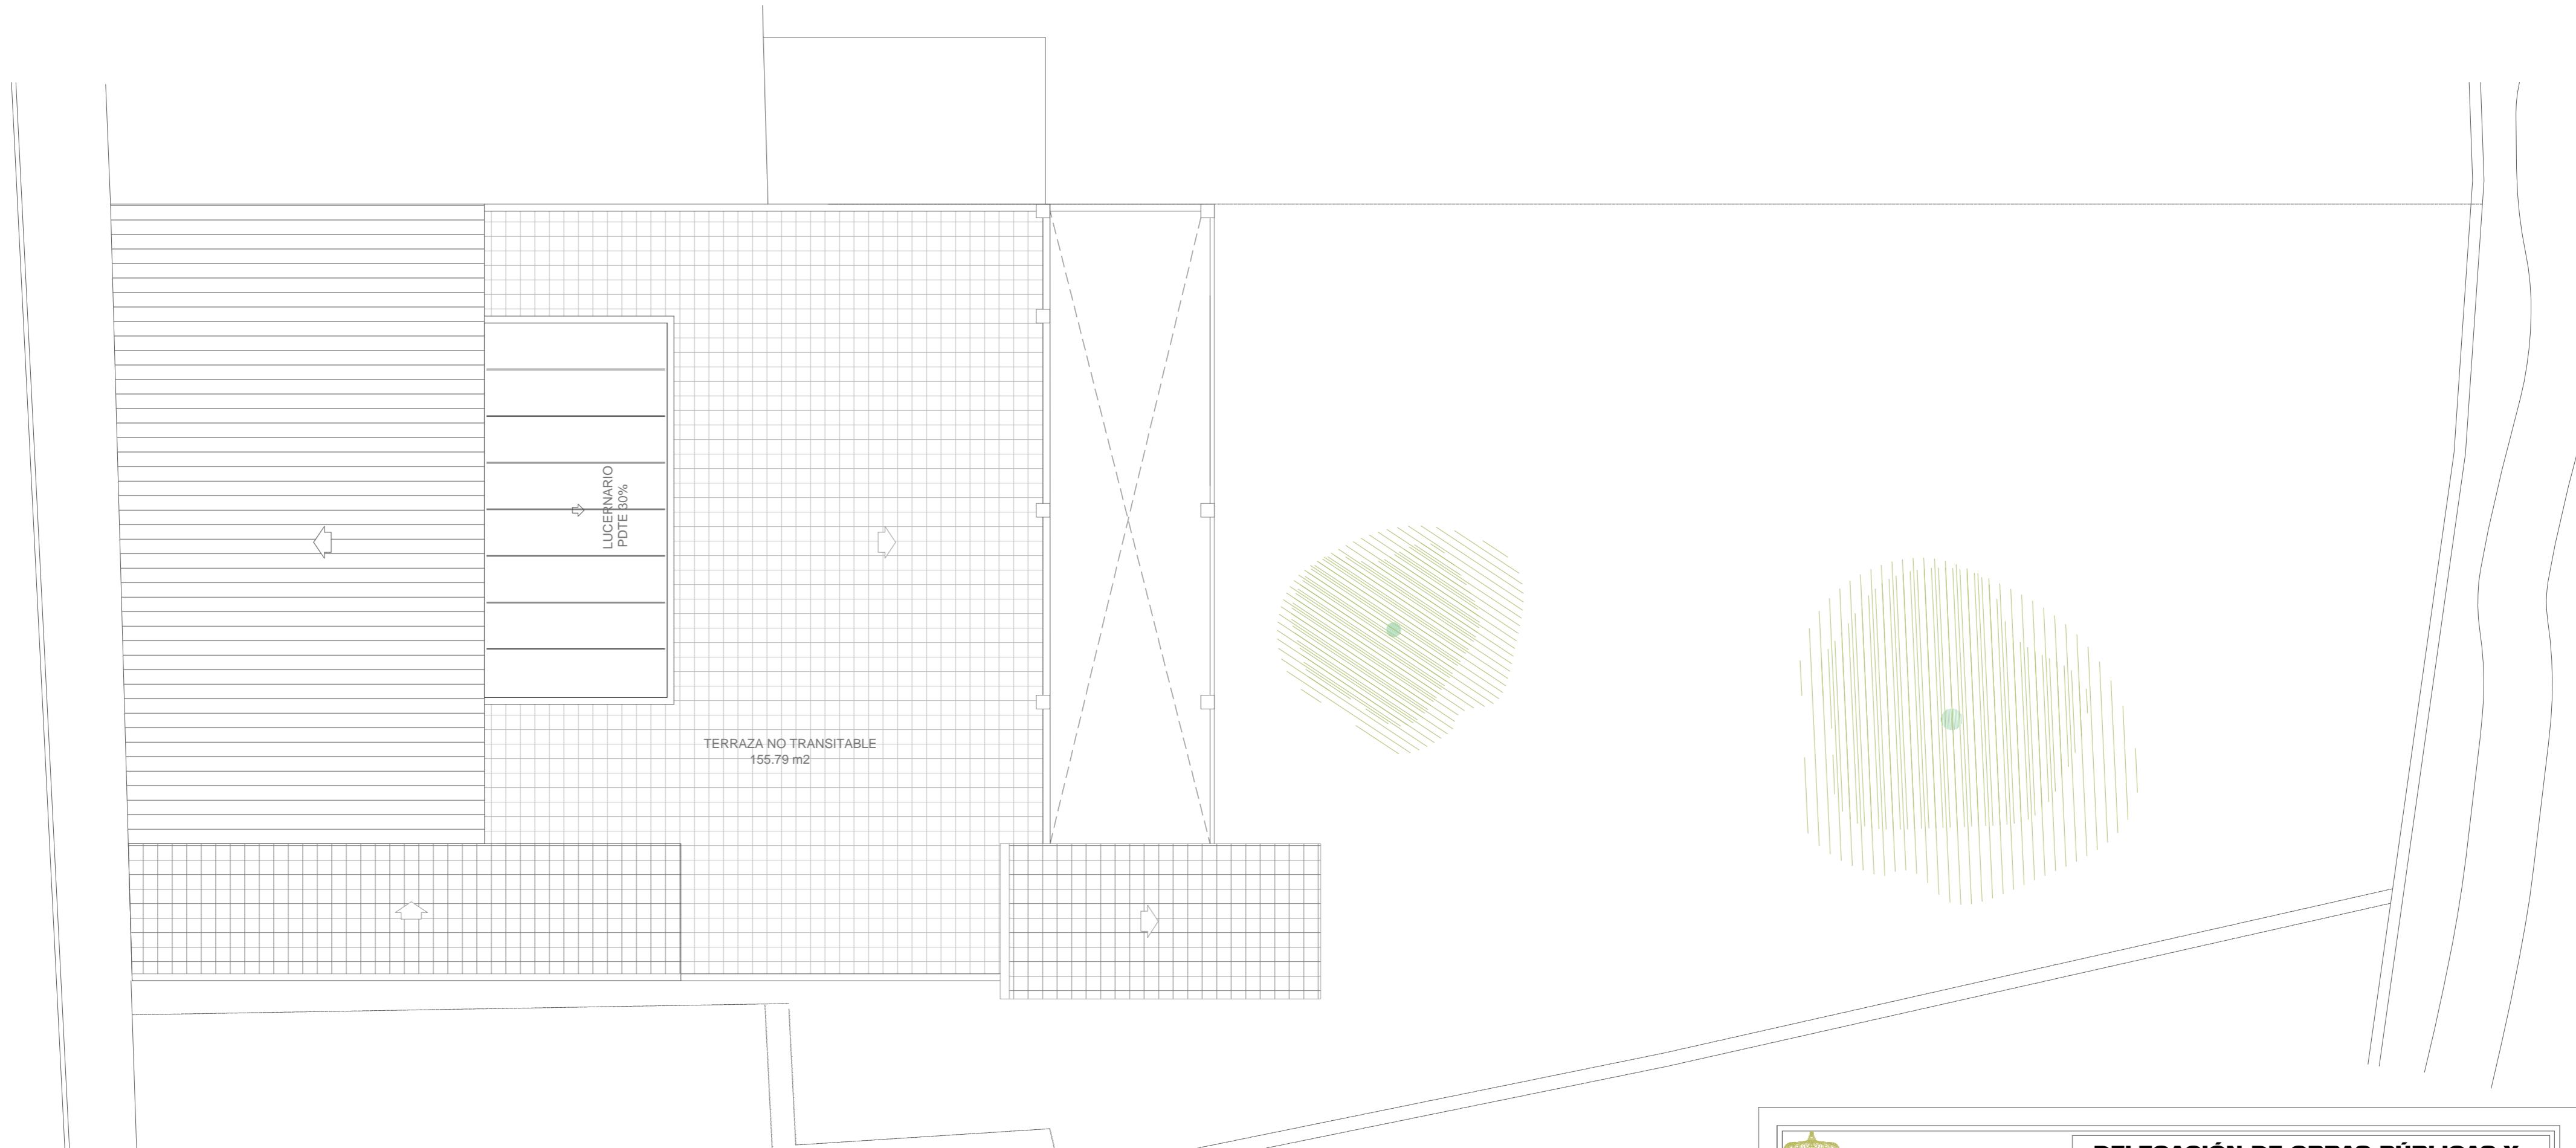

	Excma. Diputación Provincial de Granada		DELEGACIÓN DE OBRAS PÚBLICAS Y VIVIENDA	
SERVICIO DE INFRAESTRUCTURAS Y EQUIPAMIENTOS LOCALES				
REFERENCIA: 2014/2/PPOYS-125	PROYECTO: CENTRO DE DÍA DE MONTEJÍCAR. INSTALACIONES Y OTROS			
FECHA: Octubre 2015	EN	MONTEJÍCAR (GRANADA)		
PLANO N° 05	PLANO DE: PLANTA CUBIERTAS	ESCALA: 1/100		
		ARQUITECTO: RAFAEL GONZALEZ VARGAS ARQUITECTO TÉCNICO: ANTONIO DELGADO DÍAZ		
ESTUDIANTES DE ARQUITECTURA EN PRÁCTICAS ESTER ALMIRALL ROERO CRISTINA ALVAREZ GONZÁLEZ ANGELA TOMAS OLMO PAULA MARTA MARTÍNEZ PÉREZ ESTUDIANTES DE ARQUITECTURA TÉCNICA EN PRÁCTICAS ISABEL ARANDA ACEVEDO ANTONIO GONZALEZ JIMÉNEZ				



Excma. Diputación
Provincial de Granada

**DELEGACIÓN DE OBRAS PÚBLICAS Y
VIVIENDA**
SERVICIO DE INFRAESTRUCTURAS Y EQUIPAMIENTOS LOCALES

REFERENCIA:
2014/2/PPOYS-125

PROYECTO:

CENTRO DE DÍA DE MONTEJÍCAR. INSTALACIONES Y OTROS

FECHA:
Octubre 2015

EN

MONTEJÍCAR (GRANADA)

PLANO N°

07

PLANO DE:

PLANTA SEMISÓTANO. ALBAÑILERÍA


ESCALA:

1/100



ARQUITECTO:
RAFAEL GONZALEZ VARGAS
ARQUITECTO TÉCNICO:
ANTONIO DELGADO DIAZ

ESTUDIANTES DE ARQUITECTURA EN PRÁCTICAS
ESTHER ALFARO ROERO
CRISTINA ALVAREZ GUARNIDES
ANGELA TOMAS OLMO
PAULA MARTA MARTINEZ PEREZ
ESTUDIANTE DE ARQUITECTURA TÉCNICA EN PRÁCTICAS
ISABEL ARANDA ACEVEDO
ANTONIO GONZALEZ JIMÉNEZ

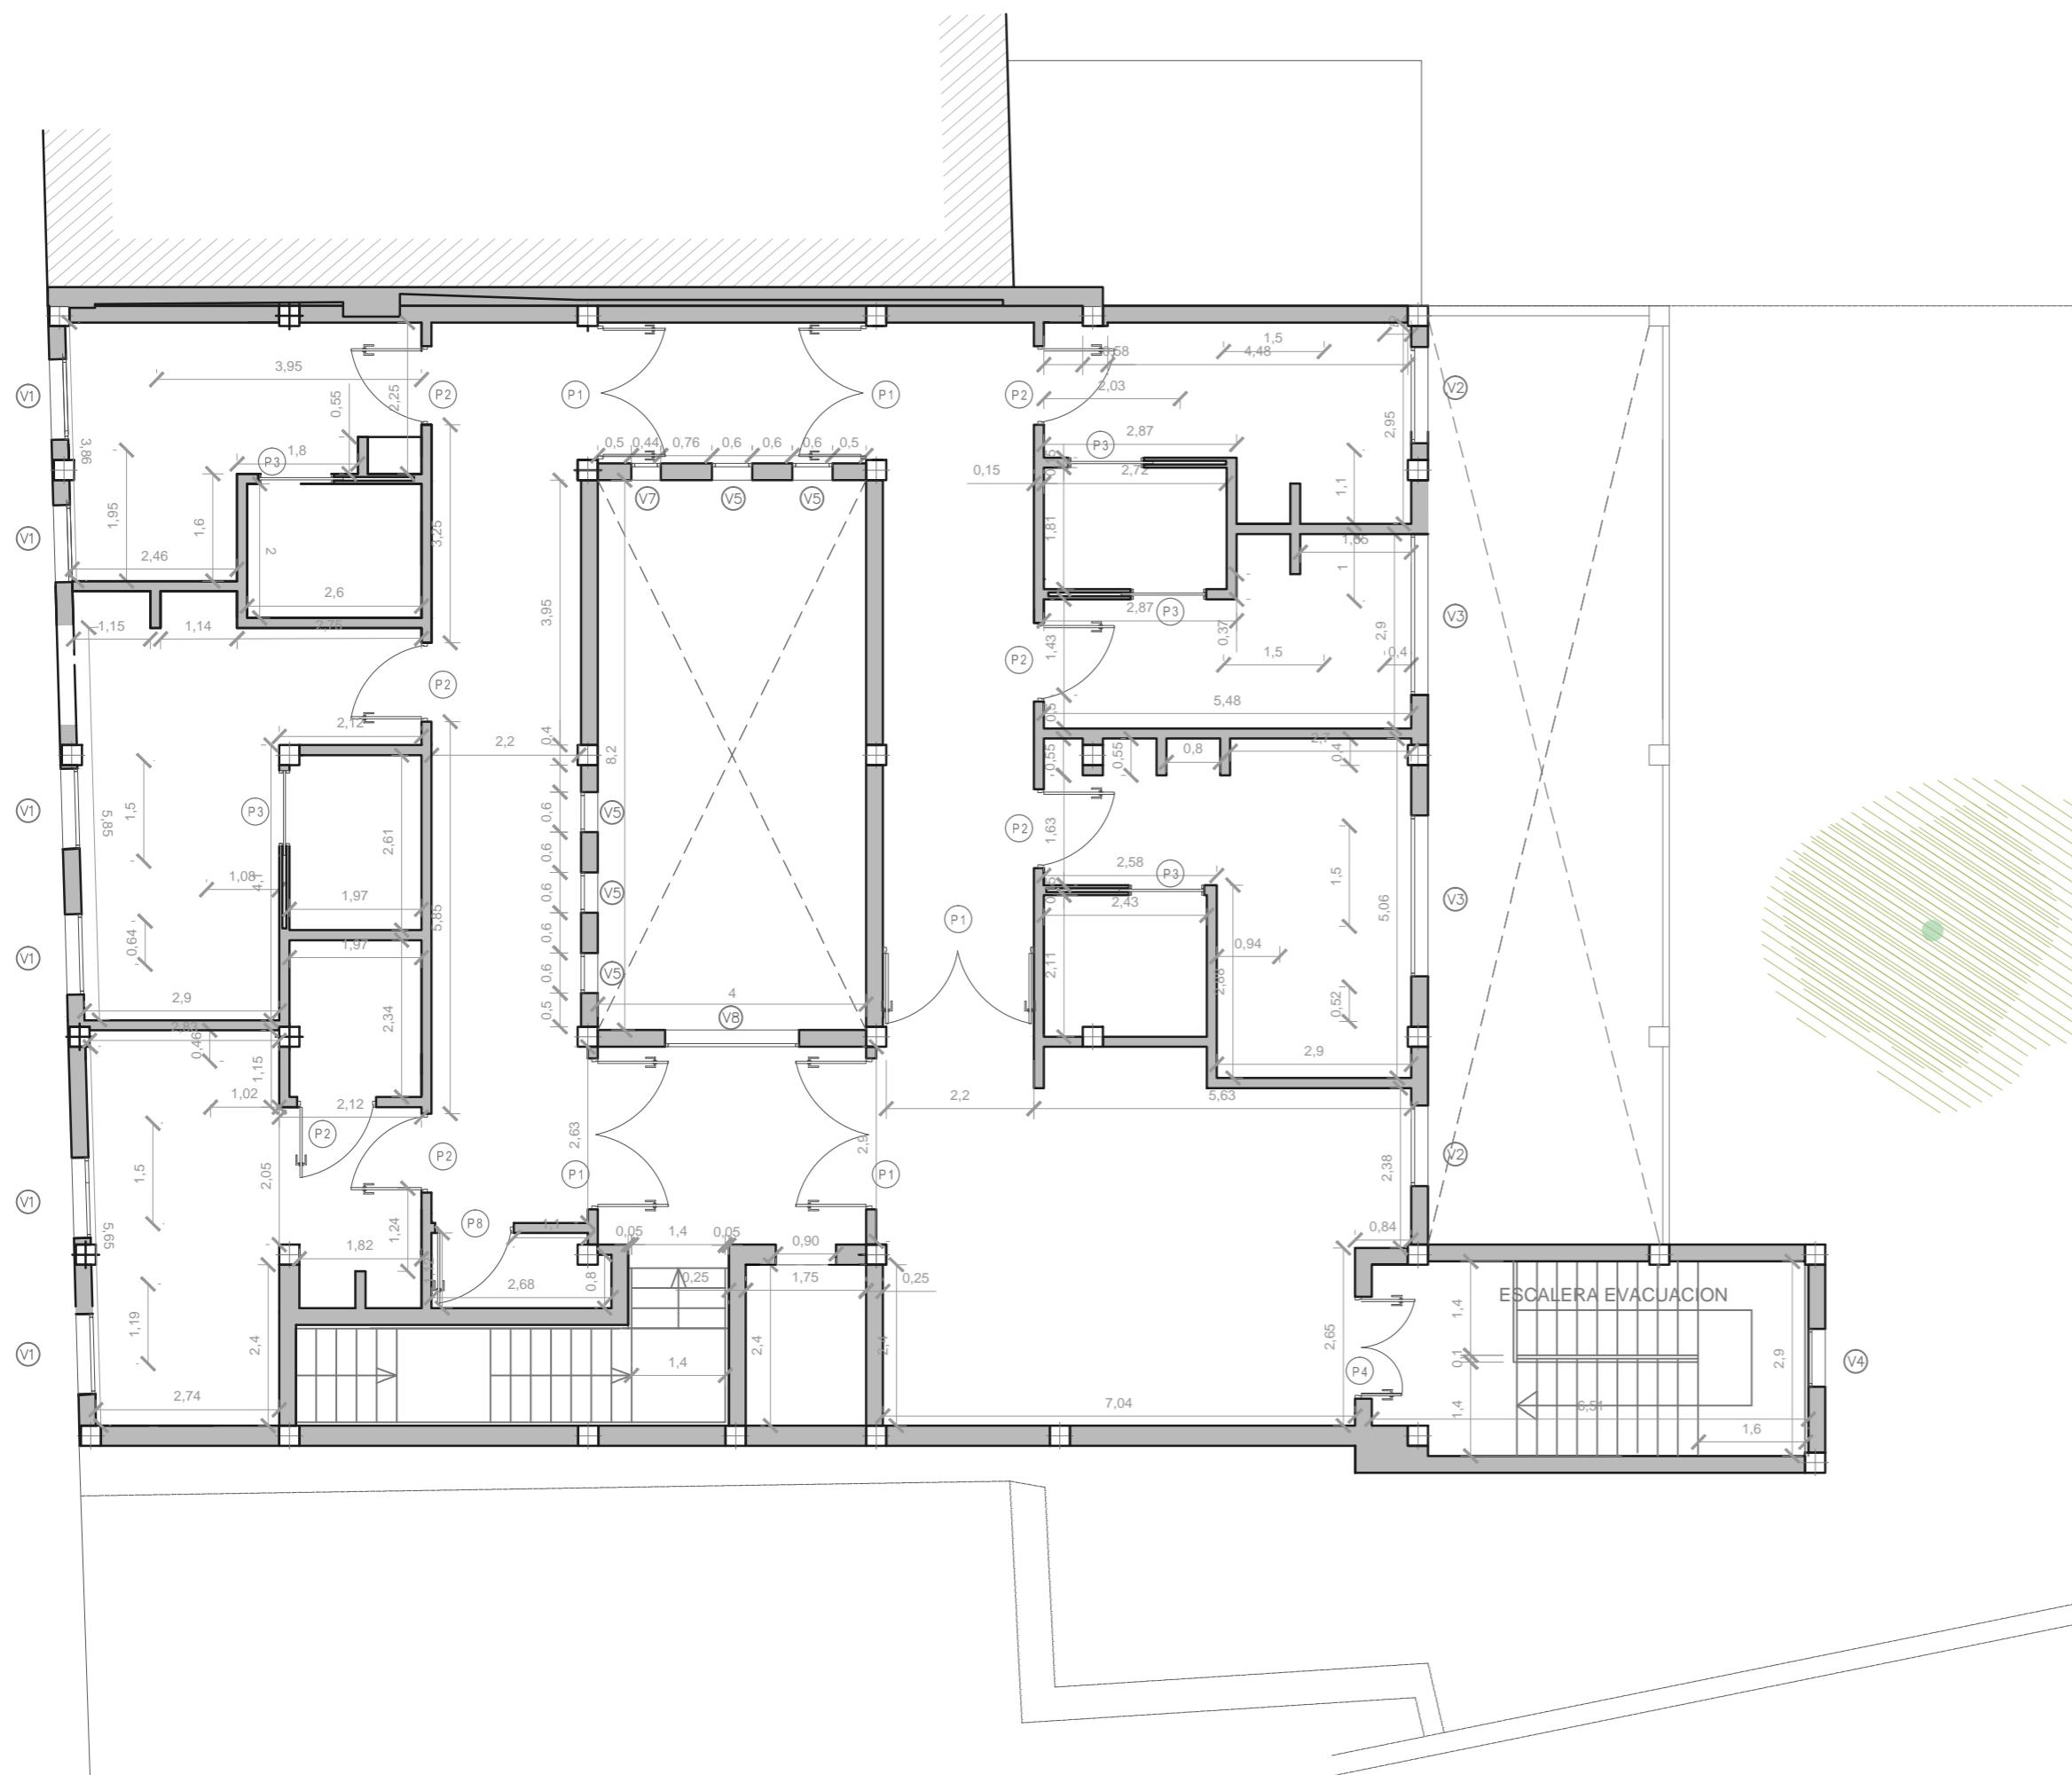

Excma. Diputación
Provincial de Granada

**DELEGACIÓN DE OBRAS PÚBLICAS Y
VIVIENDA**
SERVICIO DE INFRAESTRUCTURAS Y EQUIPAMIENTOS LOCALES

REFERENCIA:
2014/2/PPOYS-125
FECHA:
Octubre 2015

PROYECTO:
**CENTRO DE DÍA DE MONTEJÍCAR.
INSTALACIONES Y OTROS**
EN
MONTEJÍCAR (GRANADA)

PLANO N°
09

PLANO DE:
PLANTA PRIMERA. ALBAÑILERÍA
ESCALA:
1/100



ARQUITECTO:
RAFAEL GONZALEZ VARGAS
ARQUITECTO TÉCNICO:
ANTONIO DELGADO DIAZ

ESTUDIANTES DE ARQUITECTURA EN PRÁCTICAS
ESTER MOLINA ROVERO
CRISTINA ALVAREZ GONZÁLEZ
ANGELA TOMAS OLMO
PAULA MARTA MARTÍNEZ PÉREZ
ESTUDIANTE DE ARQUITECTURA TÉCNICA EN PRÁCTICAS
ISABEL ARANDA ACEVEDO
ANTONIO GONZALEZ JIMÉNEZ



Excma.Diputación
Provincial de Granada

**DELEGACIÓN DE OBRAS PÚBLICAS Y
VIVIENDA**
SERVICIO DE INFRAESTRUCTURAS Y EQUIPAMIENTOS LOCALES

REFERENCIA:
2014/2/PPOYS-125

FECHA:
Octubre 2015

PROYECTO:

CENTRO DE DÍA DE MONTEJÍCAR. INSTALACIONES Y OTROS

EN

MONTEJÍCAR (GRANADA)

PLANO N°

11

PLANO DE:

PLANTA SEMISÓTANO. ACCESIBILIDAD

ESCALA:



1/100




ARQUITECTO:
RAFAEL GONZALEZ VARGAS
ARQUITECTO TÉCNICO:
ANTONIO DELGADO DIAZ

ESTUDIANTES DE ARQUITECTURA EN PRÁCTICAS
ESTHER ALMOSA RODRIGO
CRISTINA ALVAREZ GUARNIDES
ANGELA TOMAS OLMO
PAULA MARTA MARTINEZ PEREZ
ESTUDIANTES DE ARQUITECTURA TÉCNICA EN PRÁCTICAS
ISABEL ARANDA REVERÓN
ANTONIO GONZALEZ JIMÉNEZ

PILAREJO
CALLE

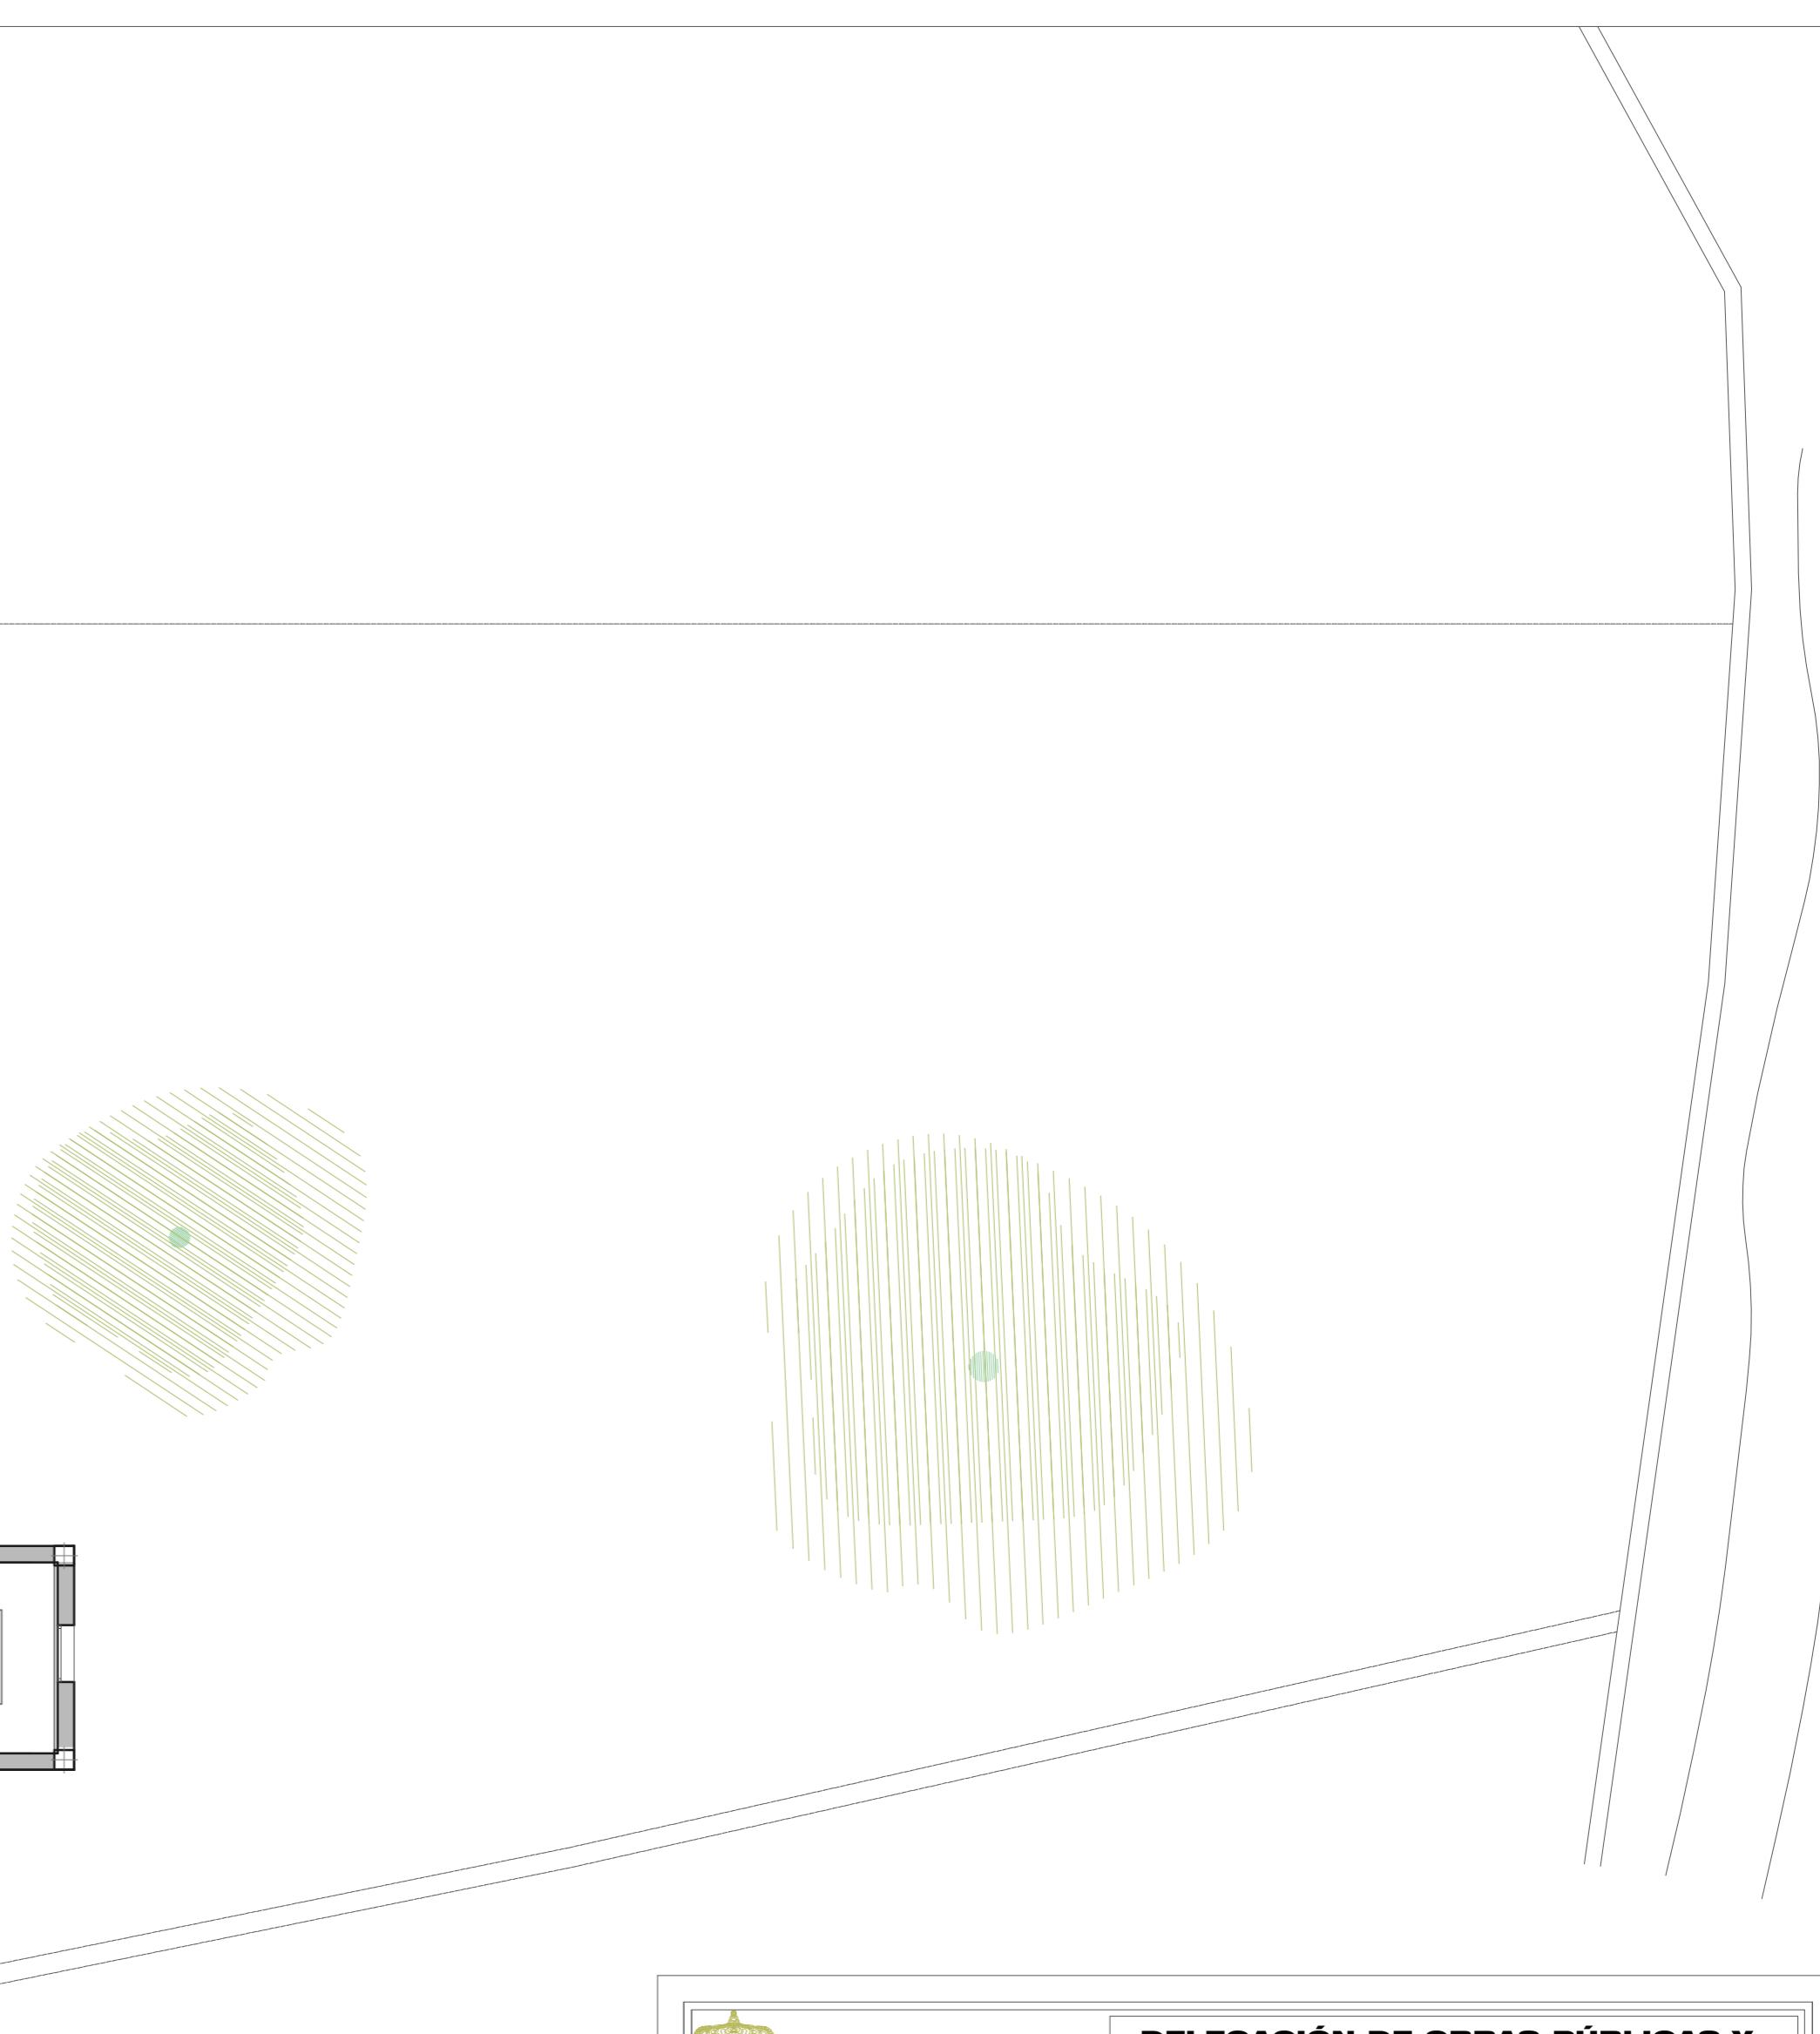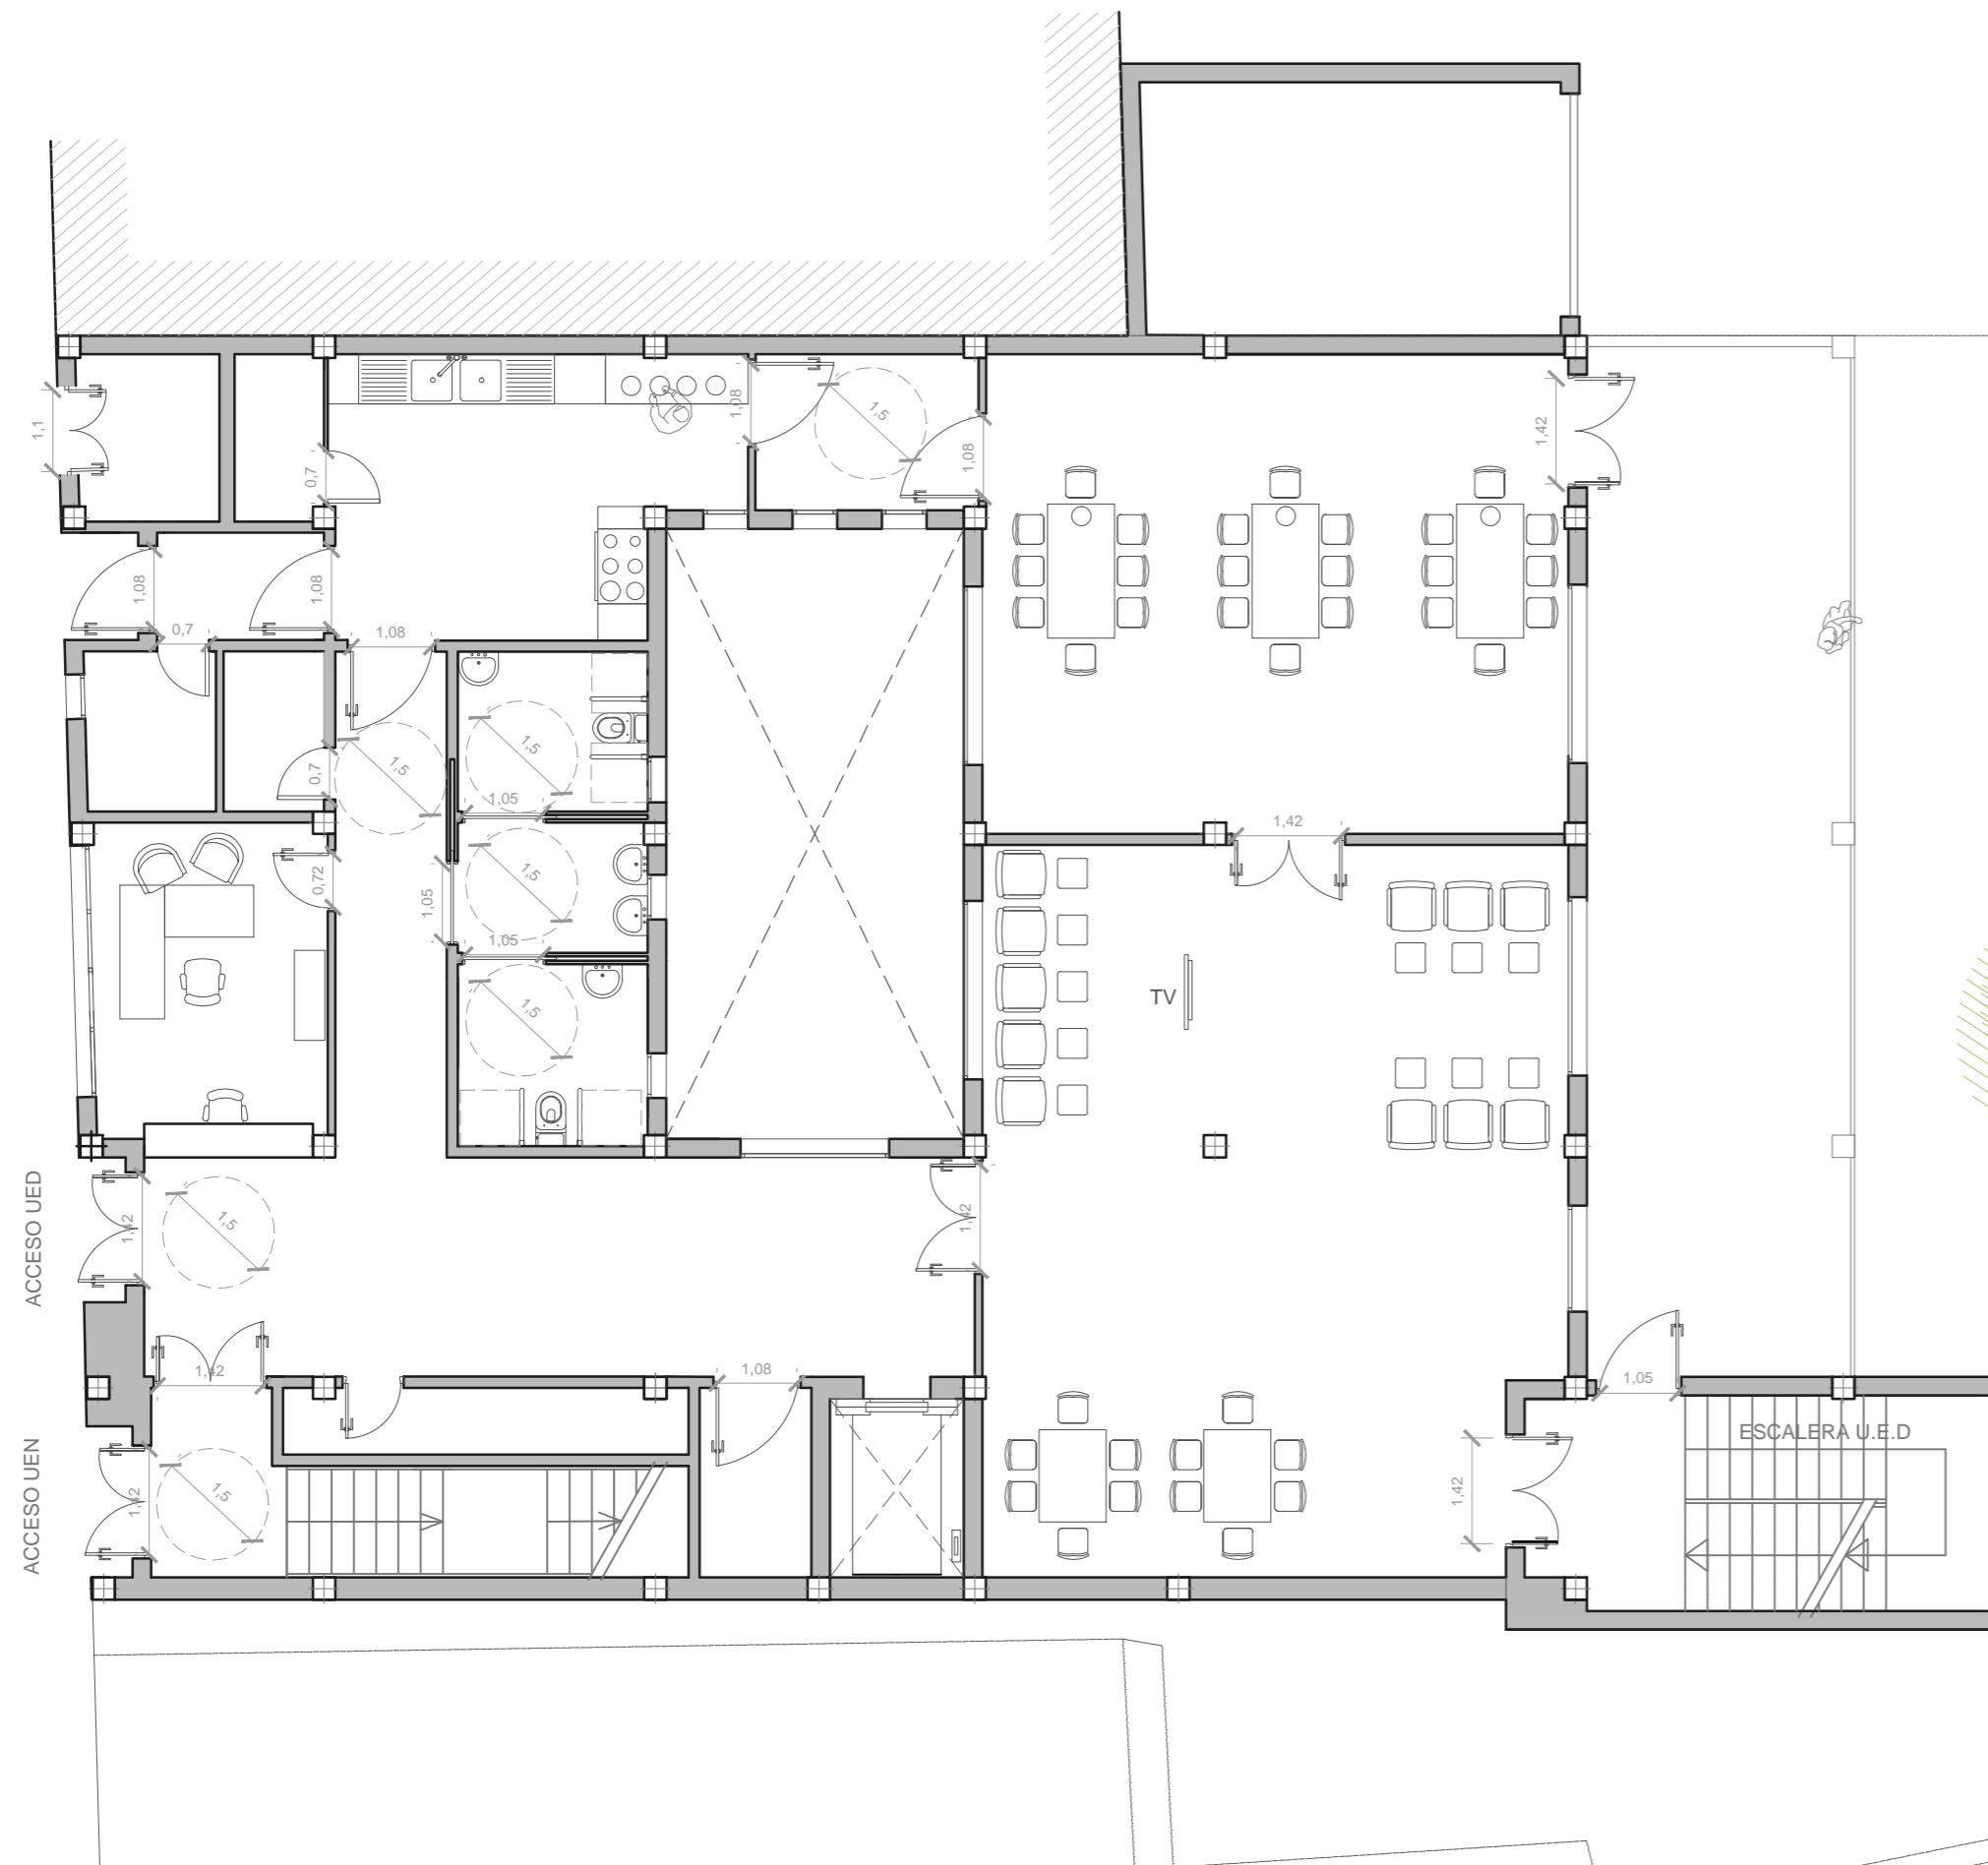

	Excma. Diputación Provincial de Granada	DELEGACIÓN DE OBRAS PÚBLICAS Y VIVIENDA
REFERENCIA: 2014/2/PPOYS-125	PROYECTO: CENTRO DE DÍA DE MONTEJÍCAR. INSTALACIONES Y OTROS	SERVICIO DE INFRAESTRUCTURAS Y EQUIPAMIENTOS LOCALES
FECHA: Octubre 2015	EN MONTEJÍCAR (GRANADA)	PLANO N° 12
PLANO DE: PLANTA BAJA. ACCESIBILIDAD	ESCALA: 1/100	
	ARQUITECTO: RAFAEL GONZALEZ VARGAS	ESTUDIANTES DE ARQUITECTURA EN PRÁCTICAS ESTHER ALFARO ROERO CRISTINA ALVAREZ GUARNIDES ANGELA TOMAS OLMO
	ARQUITECTO TÉCNICO: ANTONIO DELGADO DIAZ	PAULA MARTA MARTÍNEZ PÉREZ ESTUDIANTE DE ARQUITECTURA TÉCNICA EN PRÁCTICAS ISABEL AGUILAR REVERÓN ANTONIO GONZALEZ JIMÉNEZ

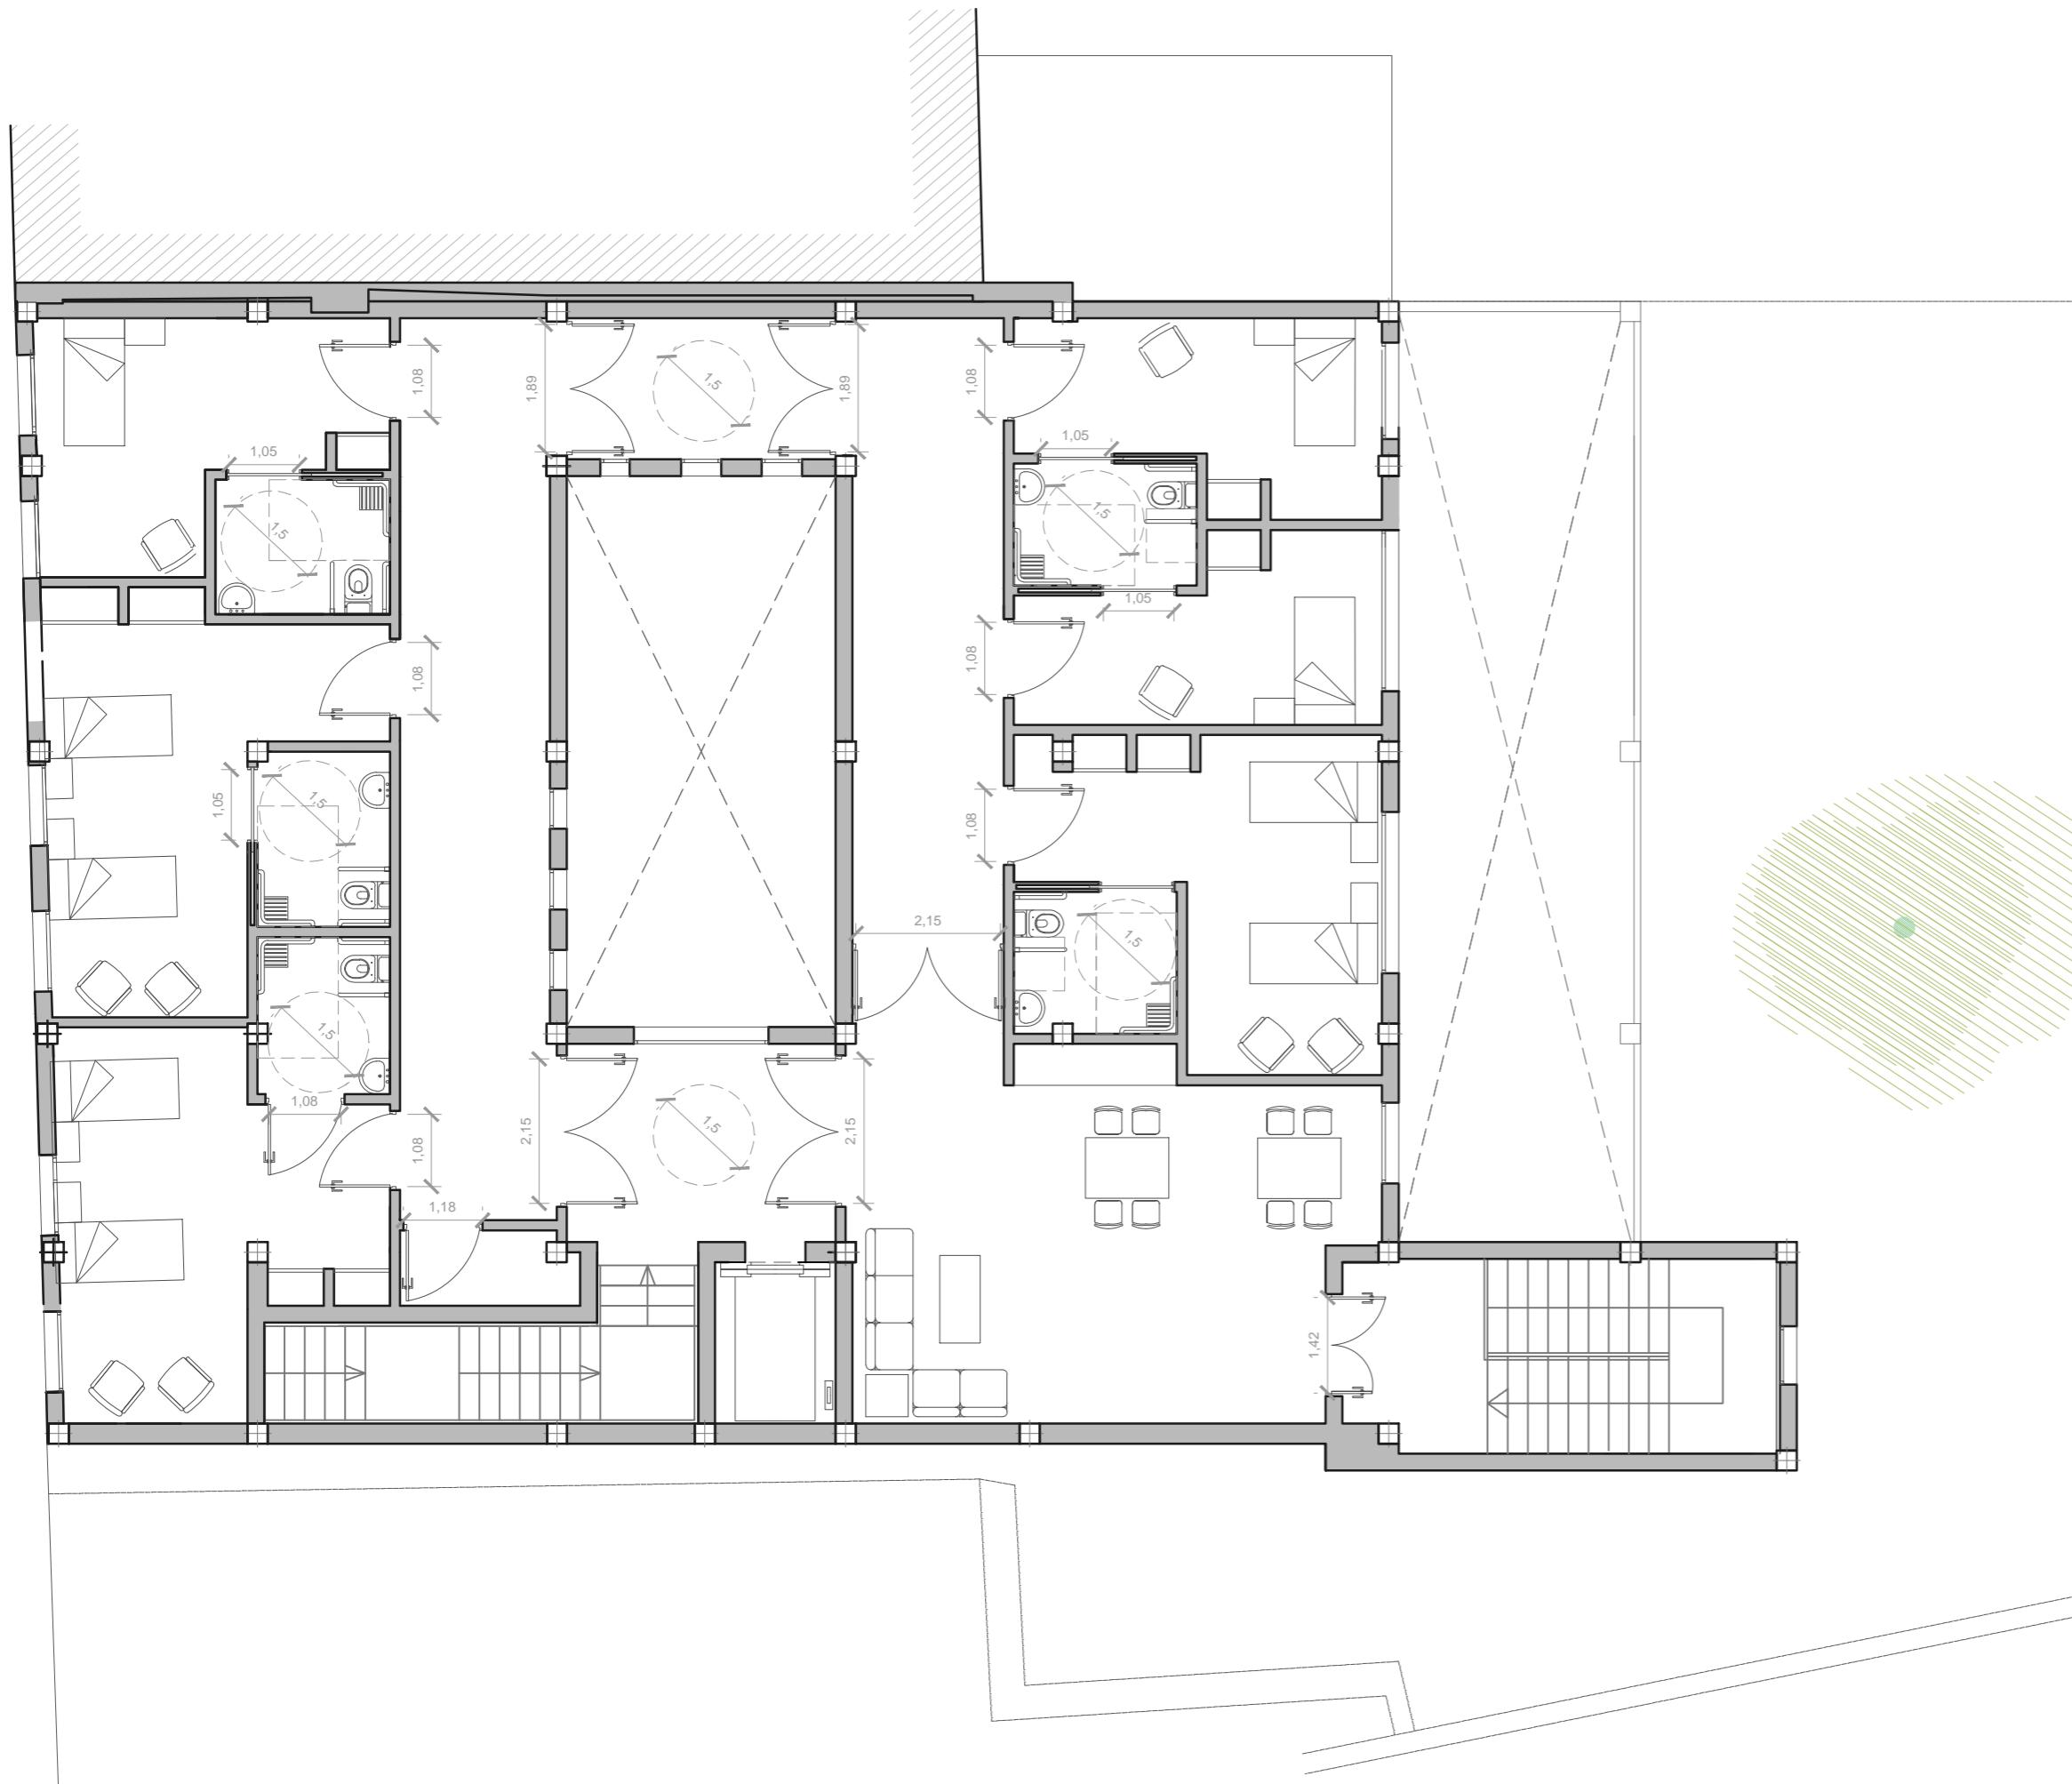

Excma. Diputación
Provincial de Granada

**DELEGACIÓN DE OBRAS PÚBLICAS Y
VIVIENDA**
SERVICIO DE INFRAESTRUCTURAS Y EQUIPAMIENTOS LOCALES

REFERENCIA:
2014/2/PPOYS-125

FECHA:
Octubre 2015

PROYECTO:
**CENTRO DE DÍA DE MONTEJÍCAR.
INSTALACIONES Y OTROS**

EN **MONTEJÍCAR (GRANADA)**

PLANO N°

13

PLANO DE:

PLANTA PRIMERA. ACCESIBILIDAD


ESCALA:

1/100



ARQUITECTO:
RAFAEL GONZALEZ VARGAS
ARQUITECTO TÉCNICO:
ANTONIO DELGADO DIAZ

ESTUDIANTES DE ARQUITECTURA EN PRÁCTICAS
ESTHER ALMUDENA RODRIGO
CRISTINA ALVAREZ GONZÁLEZ
ANGELA TOMAS OLMO
PAULA MARTA MARTÍNEZ PÉREZ
ESTUDIANTES DE ARQUITECTURA TÉCNICA EN PRÁCTICAS
ISABEL ARANDA REQUEJO
ANTONIO GONZALEZ JIMÉNEZ

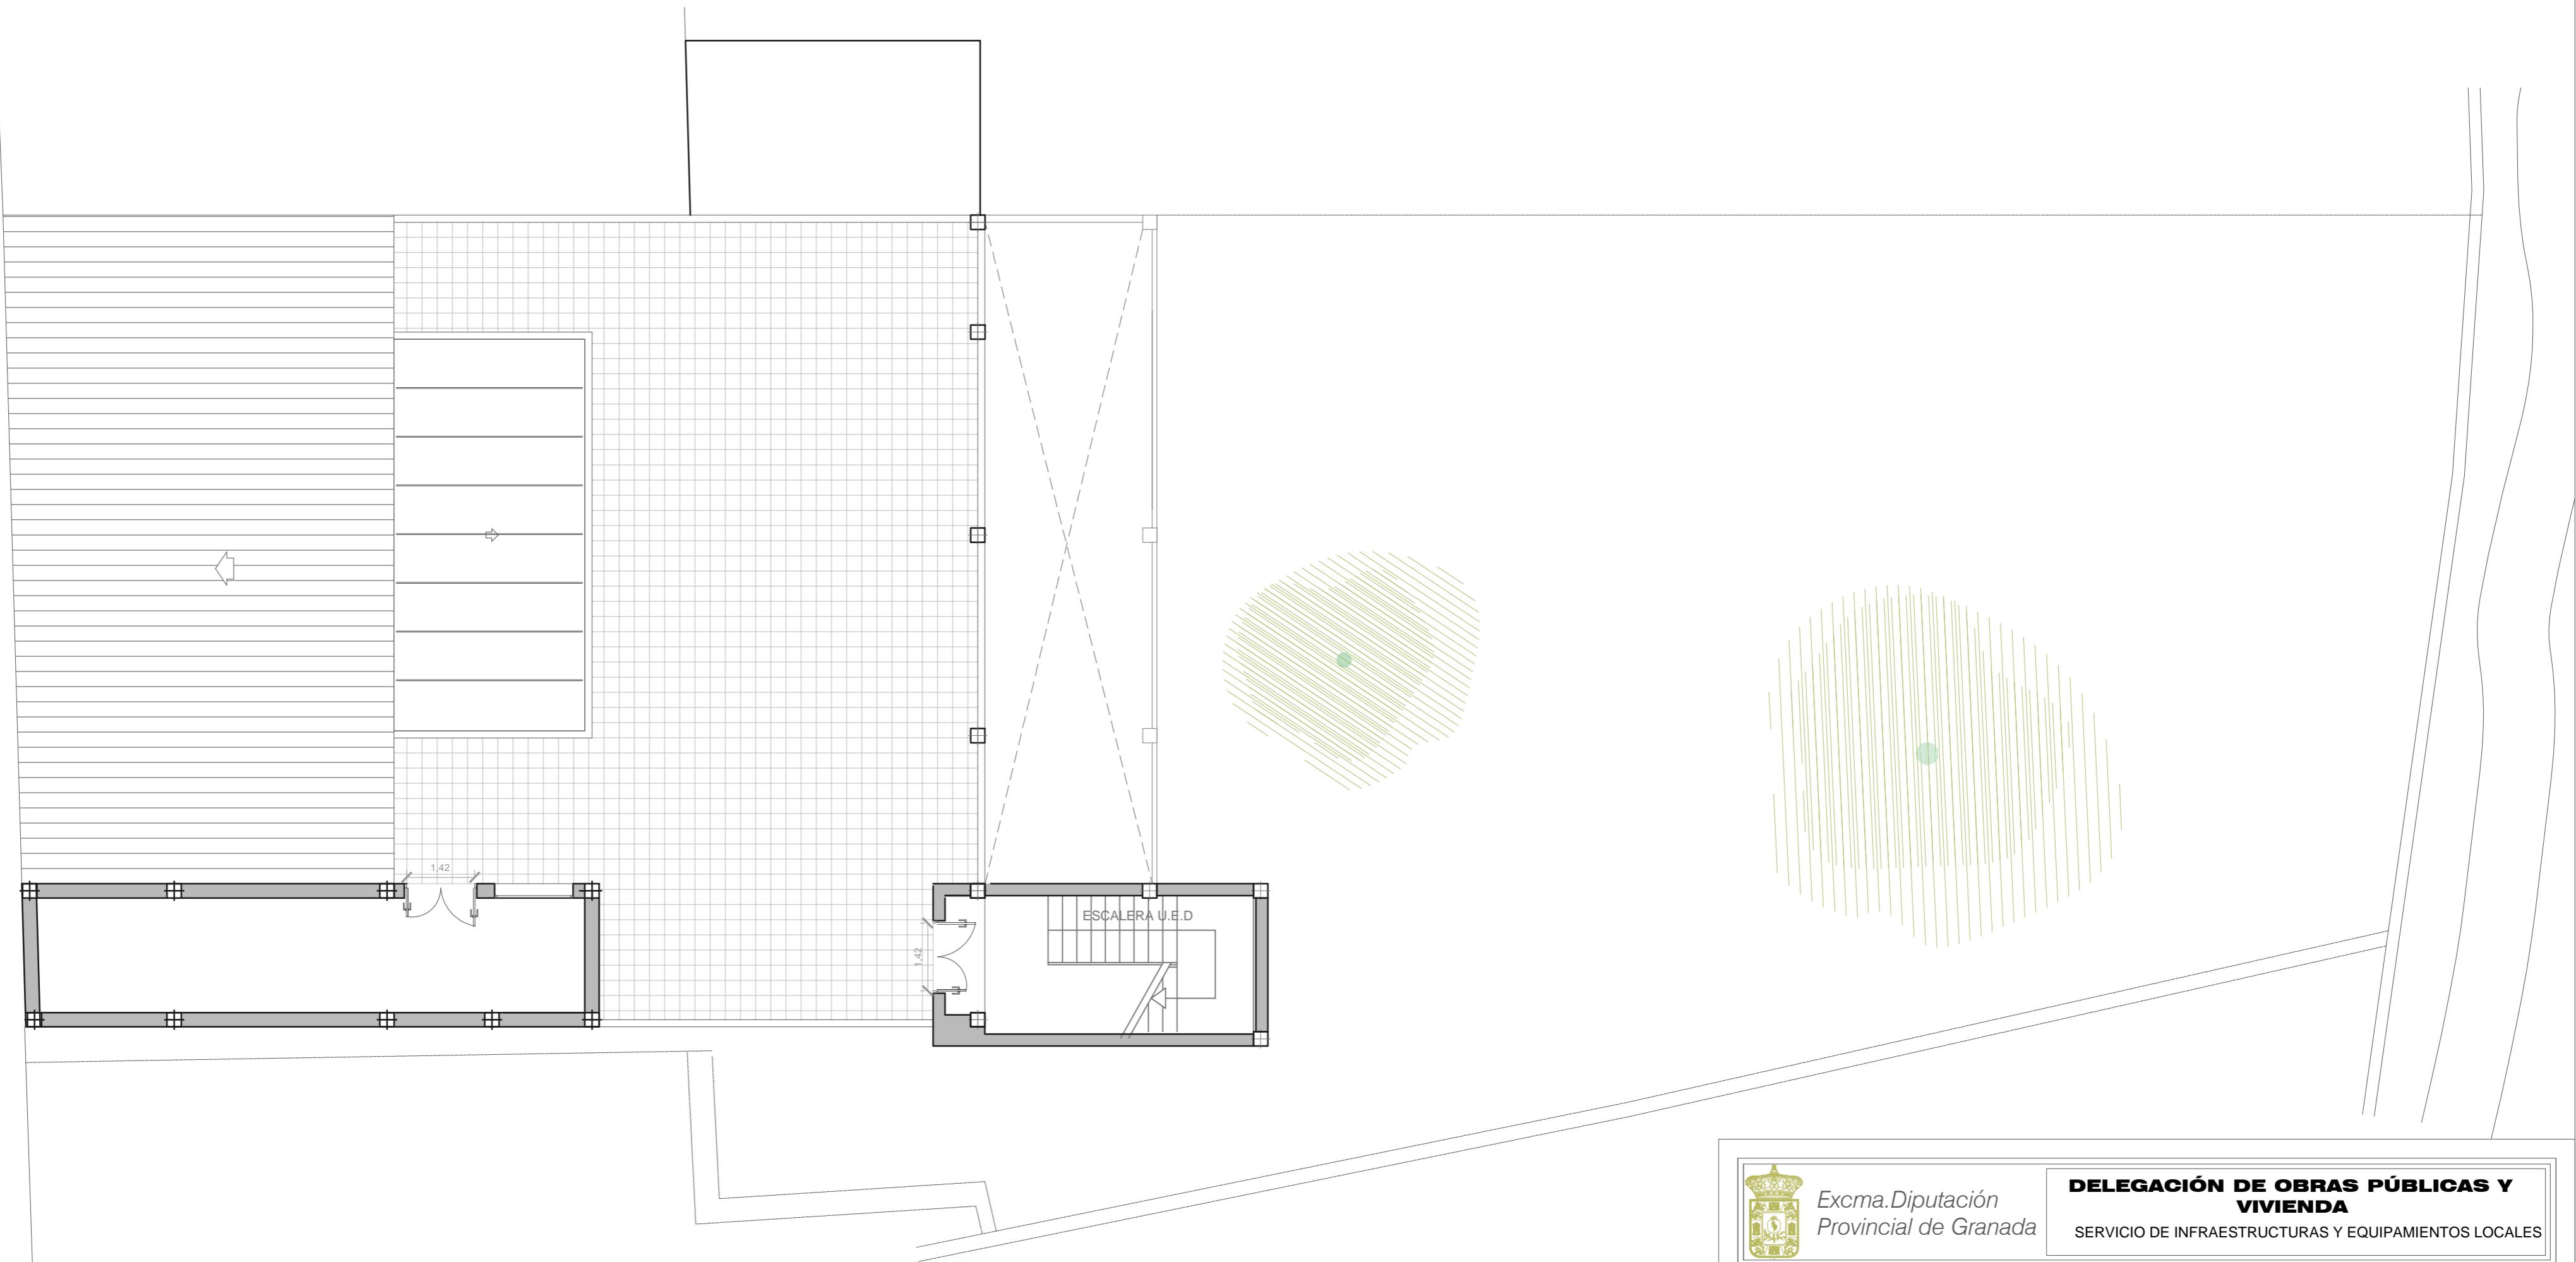


		Excma. Diputación Provincial de Granada	
		DELEGACIÓN DE OBRAS PÚBLICAS Y VIVIENDA	
		SERVICIO DE INFRAESTRUCTURAS Y EQUIPAMIENTOS LOCALES	
REFERENCIA: 2014/2/PPOYS-125	PROYECTO: CENTRO DE DÍA DE MONTEJÍCAR. INSTALACIONES Y OTROS	MONTEJÍCAR (GRANADA)	
FECHA: Octubre 2015	EN	PLANO N° 14 PLANO DE: PLANTA CUBIERTAS. ACCESIBILIDAD ESCALA: 1/100	
		ARQUITECTO: RAFAEL GONZALEZ VARGAS ARQUITECTO TÉCNICO: ANTONIO DELGADO DÍAZ	
ESTUDIANTES DE ARQUITECTURA EN PRÁCTICAS ESTEBAN ALMIRAL ROERO CRISTINA ALVAREZ GONZÁLEZ ANGELA TOMAS OLMO PAULA MARTA MARTÍNEZ PÉREZ ESTUDIANTE DE ARQUITECTURA TÉCNICA EN PRÁCTICAS ISABEL ARANDA ACEVEDO ANTONIO GONZALEZ JIMÉNEZ			



REFERENCIA	P1	P2	P3	P4	P5	P6	P7	P8	P9	P10
UNIDADES	5	8	14	11	4	7	1	8	2	1
CARPINTERIA INTERIOR										
MATERIAL	METALICA CORTAFUEGOS CON SISTEMA ANTIPANICO	MADERA	MADERA	METALICA CORTAFUEGOS CON SISTEMA ANTIPANICO	ALUMINIO O PVC LACADO COLOR	MADERA	MADERA	MELAMINA EI-45	CHAPA USA	CHAPA REJILLA
TIPO	ABATIBLE	ABATIBLE	CORREDERA	ABATIBLE	ABATIBLE	ABATIBLE	ABATIBLE	ABATIBLE	ABATIBLE	ABATIBLE

REFERENCIA	V1	V2	V3	V4	V5	V6	V7
UNIDADES	6	3	6	3	16	1	1
CARPINTERIA DE ALUMINIO							
MATERIAL	FIJA	CORREDERA	CORREDERA	FIJA	FIJA	CORREDERA	FIJA
TIPO							

REFERENCIA	V8	V9	V10	V11
UNIDADES	3	4	2	1
CARPINTERIA DE ALUMINIO				
MATERIAL	CORREDERA	CORREDERA	FIJA	CORREDERA
TIPO				

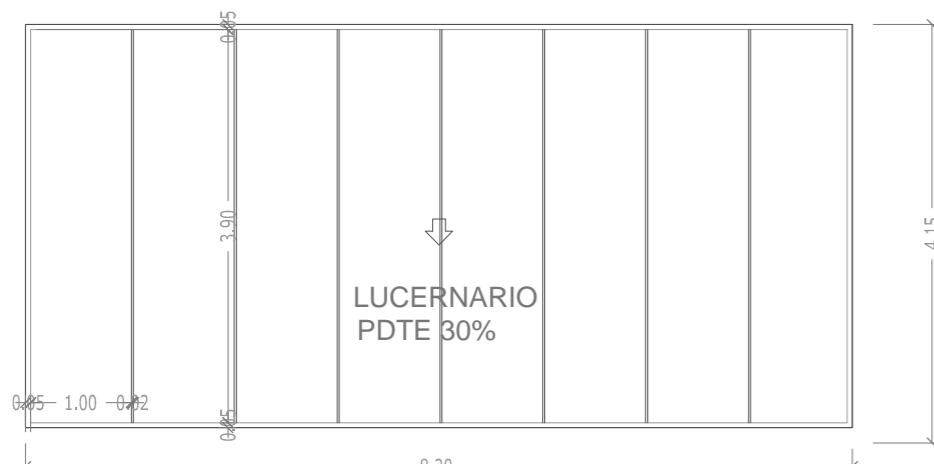

Excma. Diputación Provincial de Granada DELEGACIÓN DE OBRAS PÚBLICAS Y VIVIENDA SERVICIO DE INFRAESTRUCTURAS Y EQUIPAMIENTOS LOCALES		
REFERENCIA:	PROYECTO:	
2014/2/PPOYS-125	CENTRO DE DÍA DE MONTEJÍCAR. INSTALACIONES Y OTROS	
FECHA:	EN	
Octubre 2015	MONTEJÍCAR (GRANADA)	
PLANO N°	PLANO DE:	ESCALA:
15	MEMORIA DE CARPINTERÍA	1/75
ARQUITECTO: RAFAEL GONZALEZ VARGAS		ESTUDIANTES DE ARQUITECTURA EN PRÁCTICAS
ARQUITECTO TÉCNICO: ANTONIO DELGADO DIAZ		ESTUDIANTES DE ARQUITECTURA EN PRÁCTICAS
		CRISTINA ALVAREZ GONZALEZ
		ANGELA TOMAS OLMO
		PAULA MARTA MARTINEZ PEREZ
		ISABEL ARANDA ACEVEDO
		ANTONIO GONZALEZ JIMÉNEZ

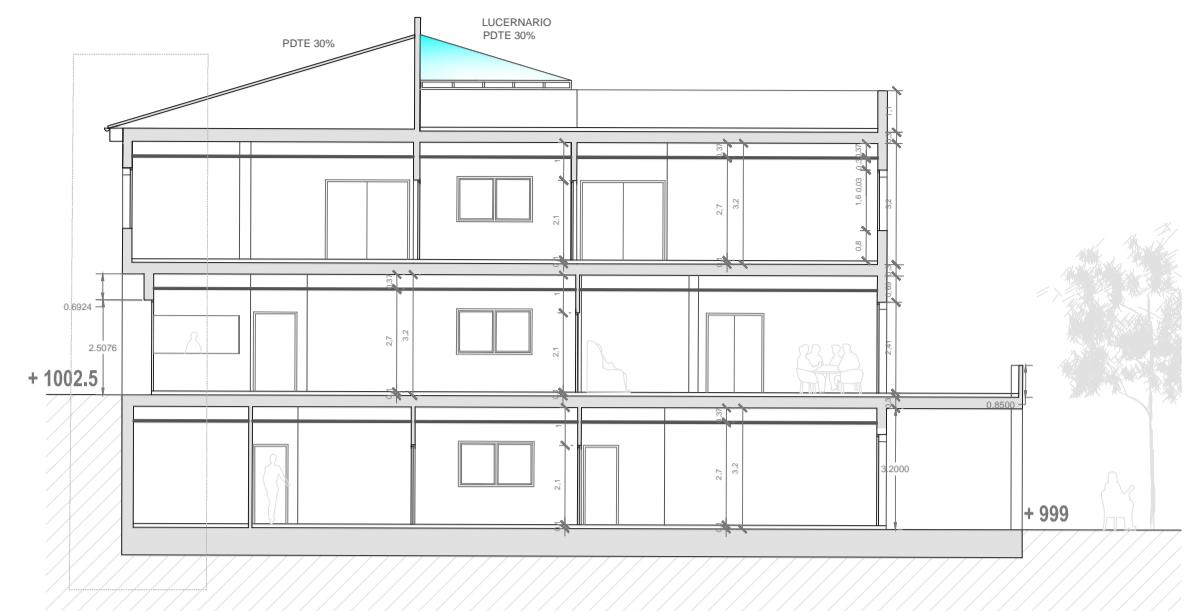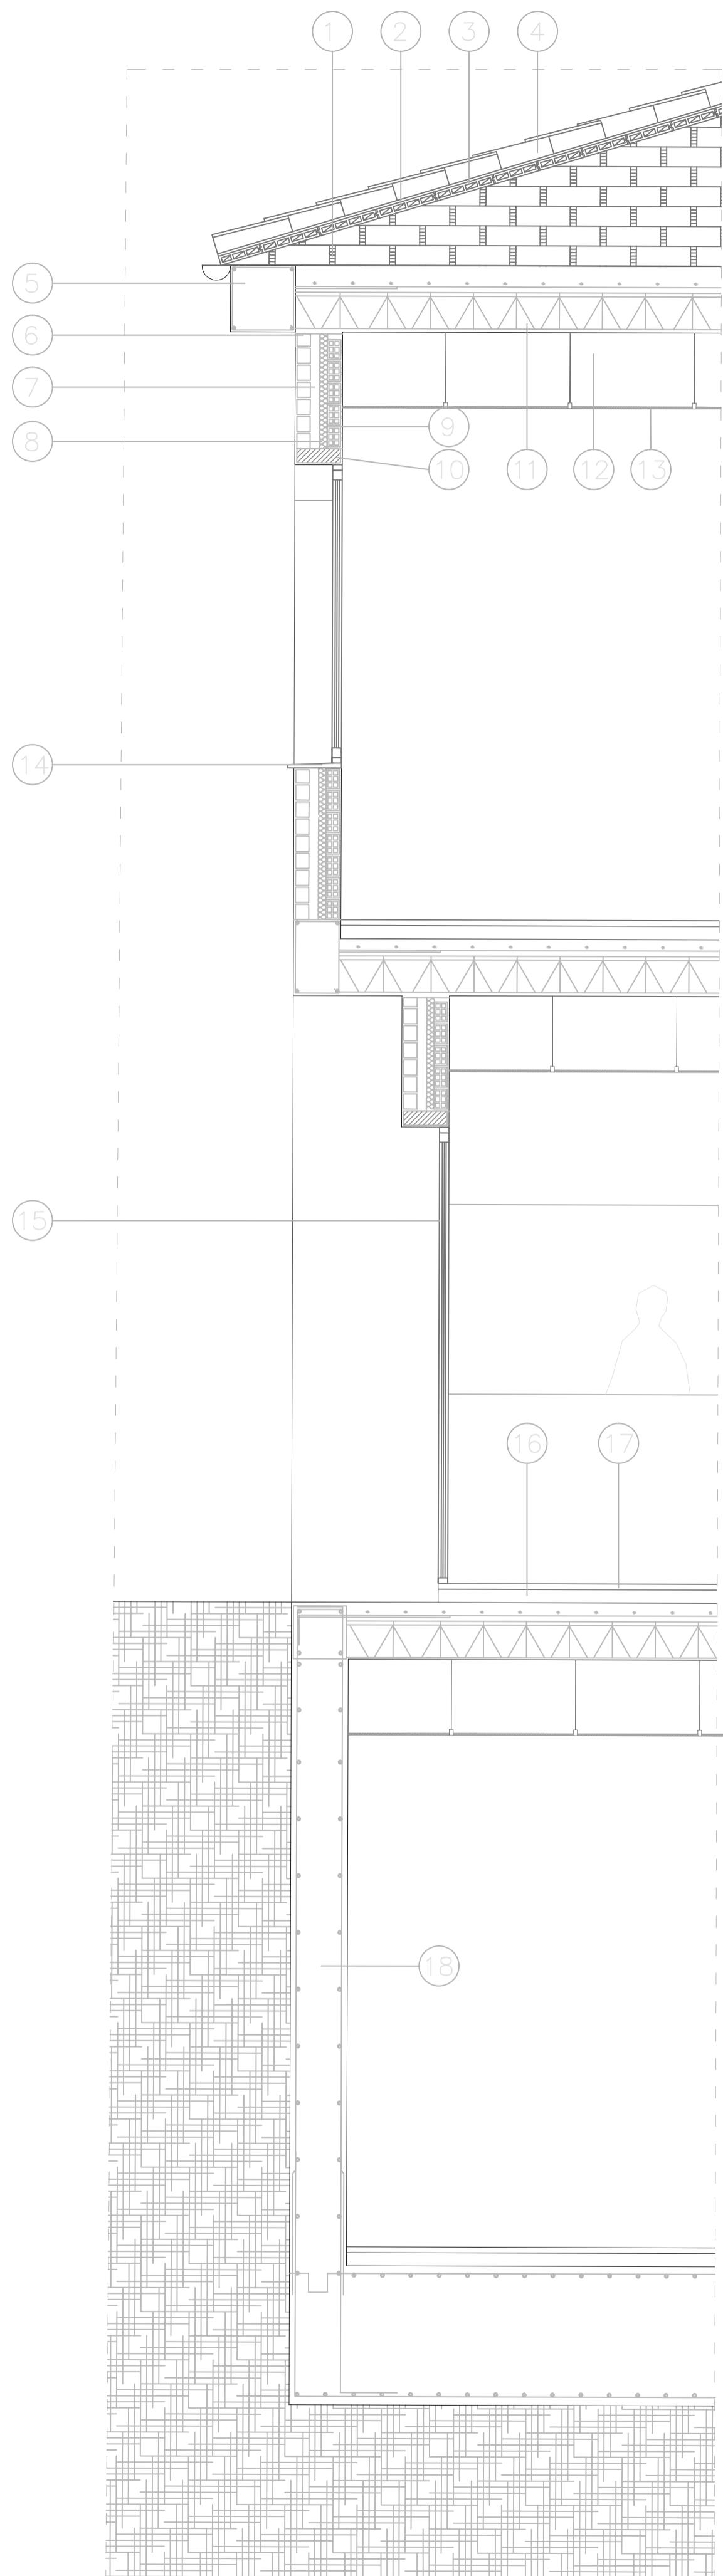

DETALLE SECCIÓN

- 1.- TABICÓN ALIGERADO DE LADRILLO H/D
- 2.- TABLERO MACHIEMBRADO
- 3.- CAPA DE COMPRESIÓN DE 30 mm
- 4.- TEJA CERÁMICA CURVA DE 40X19 cm
- 5.- ZUNCHO HORMIGÓN ARMADO S.P.
- 6.- CÍTARA DE LADRILLO PERFORADO
- 7.- CÁMARA DE AIRE $e=5$ cm
- 8.- AISLAMIENTO POLIURETANO PROYECTADO 3 cm
- 9.- TABICÓN ALIGERADO DE LADRILLO H/D
- 10.- Dintel de hormigón prefabricado
- 11.- FORJADO UNIDIRECCIONAL
- 12.- HUECO PARA INSTALACIONES
- 13.- Falso techo escayola liso
- 14.- CARPINTERIA MADERA DE IROKO
- 15.- Falso techo escayola liso
- 16.- HUECO PARA INSTALACIONES
- 17.- FORJADO UNIDIRECCIONAL
- 18.- REVESTIMIENTO DE YESO
- 19.- REVESTIMIENTO MONOCAPA FRATAJADO COLOR
- 20.- ALFEIZAR DE PIEDRA ARTIFICIAL
- 21.- CAPA DE GRAVA
- 22.- SOLERA DE HORMIGÓN ARMADO
- 23.- MORTERO DE AGARRE PORCELANICO Y SOLERIA DE GRES PORCELANICO
- 24.- Dintel de hormigón prefabricado
- 25.- TERRENO ESTABILIZADO
- 26.- ARMADURA CIMENTACIÓN
- 27.- ZAPATA AISLADA
- 28.- MORTERO DE AGARRE BALDOSA
- 29.- ACERADO BALDOSA HIDRAULICA
- 30.- BORDILLO DE HORMIGON
- 31.- PAVIMENTO CALZADA

	Excmo. Diputación Provincial de Granada	DELEGACIÓN DE OBRAS PÚBLICAS Y VIVIENDA
		SERVICIO DE INFRAESTRUCTURAS Y EQUIPAMIENTOS LOCALES
REFERENCIA: 2014/2/PPOYS-125	PROYECTO: CENTRO DE DÍA DE MONTEJÍCAR. INSTALACIONES Y OTROS	
FECHA: Octubre 2015	EN MONTEJÍCAR (GRANADA)	
PLANO N° 16	PLANO DE: SECCIÓN CONSTRUCTIVA	ESCALA: 1/25
	ARQUITECTO: RAFAEL GONZALEZ VARGAS	ESTUDIANTES DE ARQUITECTURA EN PRÁCTICAS ESTHER GONZÁLEZ ROMERO CRISTINA ALVAREZ BENAVIDES ÁNGELA GARCÍA OLMO PAULA MARTA MARTÍNEZ PÉREZ
	ARQUITECTO TÉCNICO: ANTONIO DELGADO DIAZ	ESTUDIANTE DE ARQUITECTURA TÉCNICA EN PRÁCTICAS ISABEL ARANDA ACEVEDO ANTONIO GONZÁLEZ JIMÉNEZ